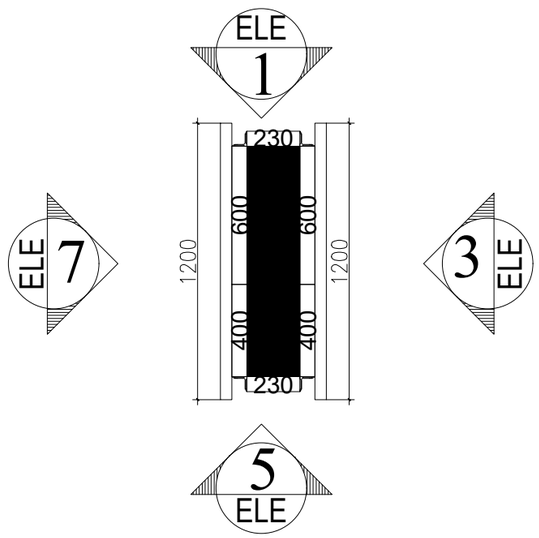

SW3(230X1000)

H=2500 MM

PLAN

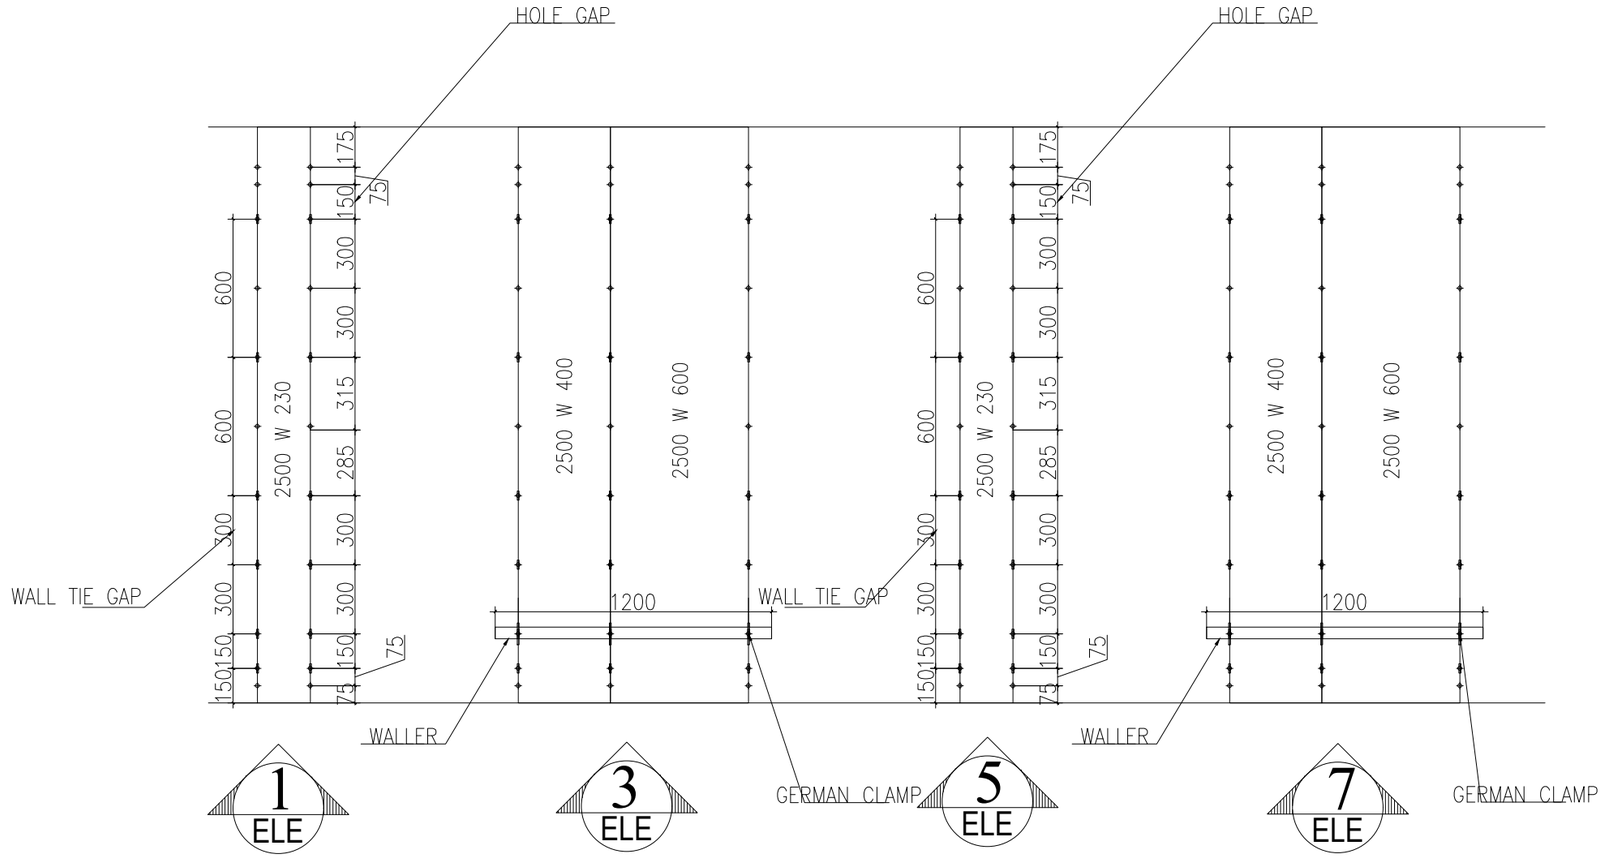

ELEVATION

REV.	DATE	DESCRIPTION	BY	CHKD.

SS ALUMINIUM FORMWORK
YOUR FORMWORK SPECIALIST

CLIENT - MARCO GROUP

PROJECT -

TITLE - COLUMN WORKING

DWG.NO:- SS-AL-CW-01

SCALE	DATE	REV.
N.T.S	27-05-2025	00
DRAWN	CHECKED	APPROVED
MS	DJ	A.K.