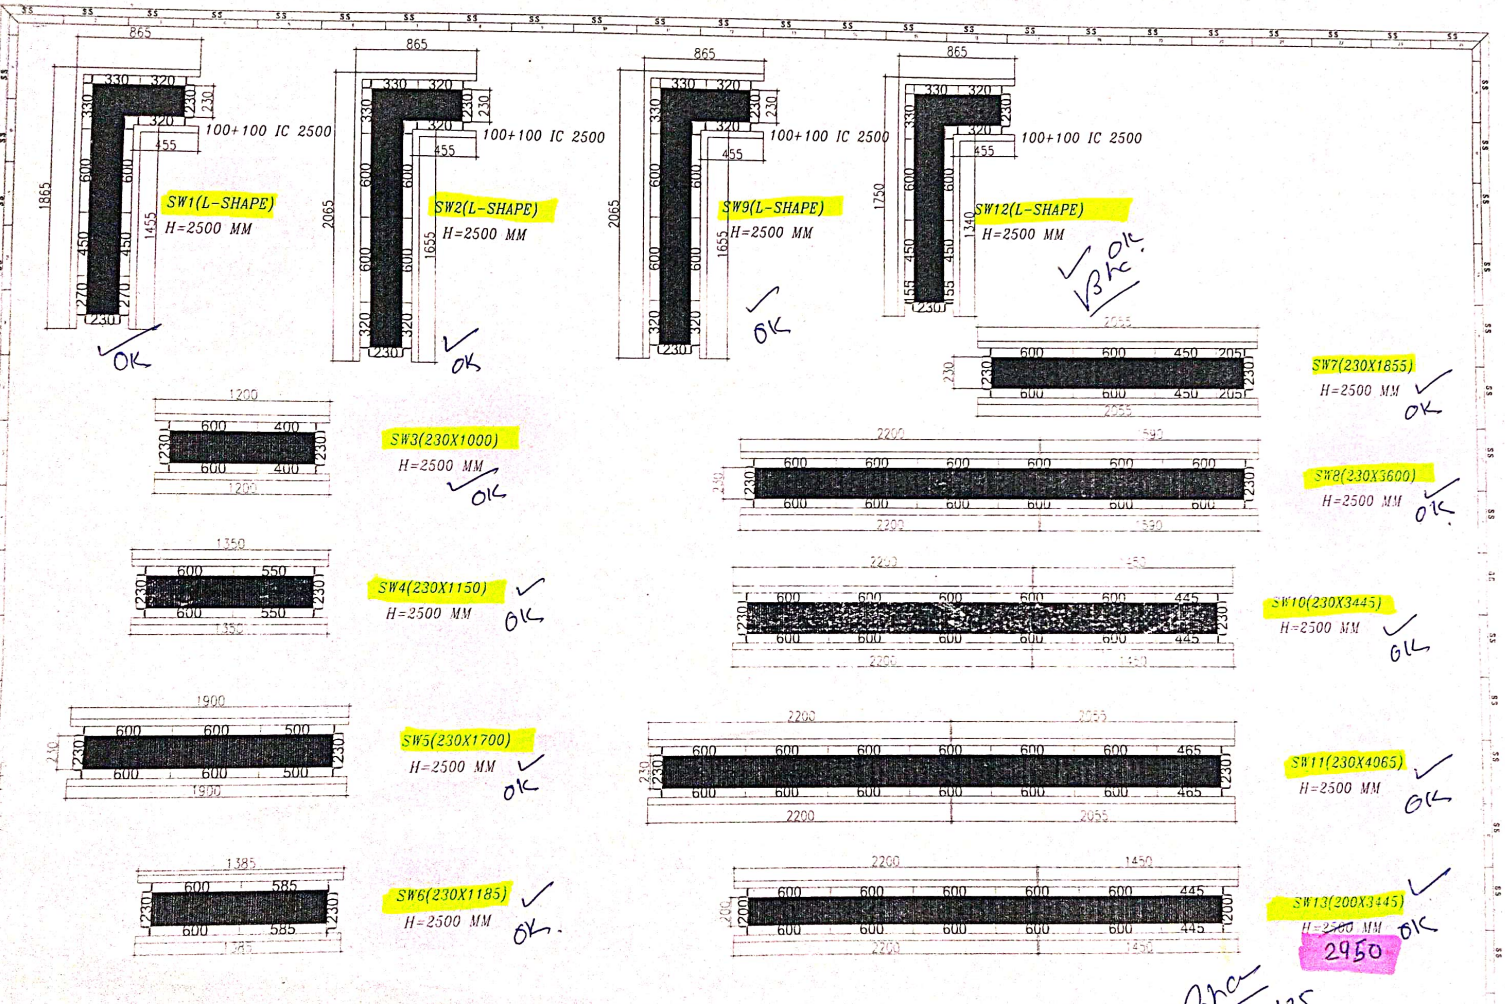

SS ALUMINIUM FORMWORK

CLIENT - MARCO GROUP

PROJECT -

TITLE - COLUMN WORKING

DWG.NO.- SS-AL-CW-01

SCALE | DATE | REV

DRAWN | CHECKED | APPROVED