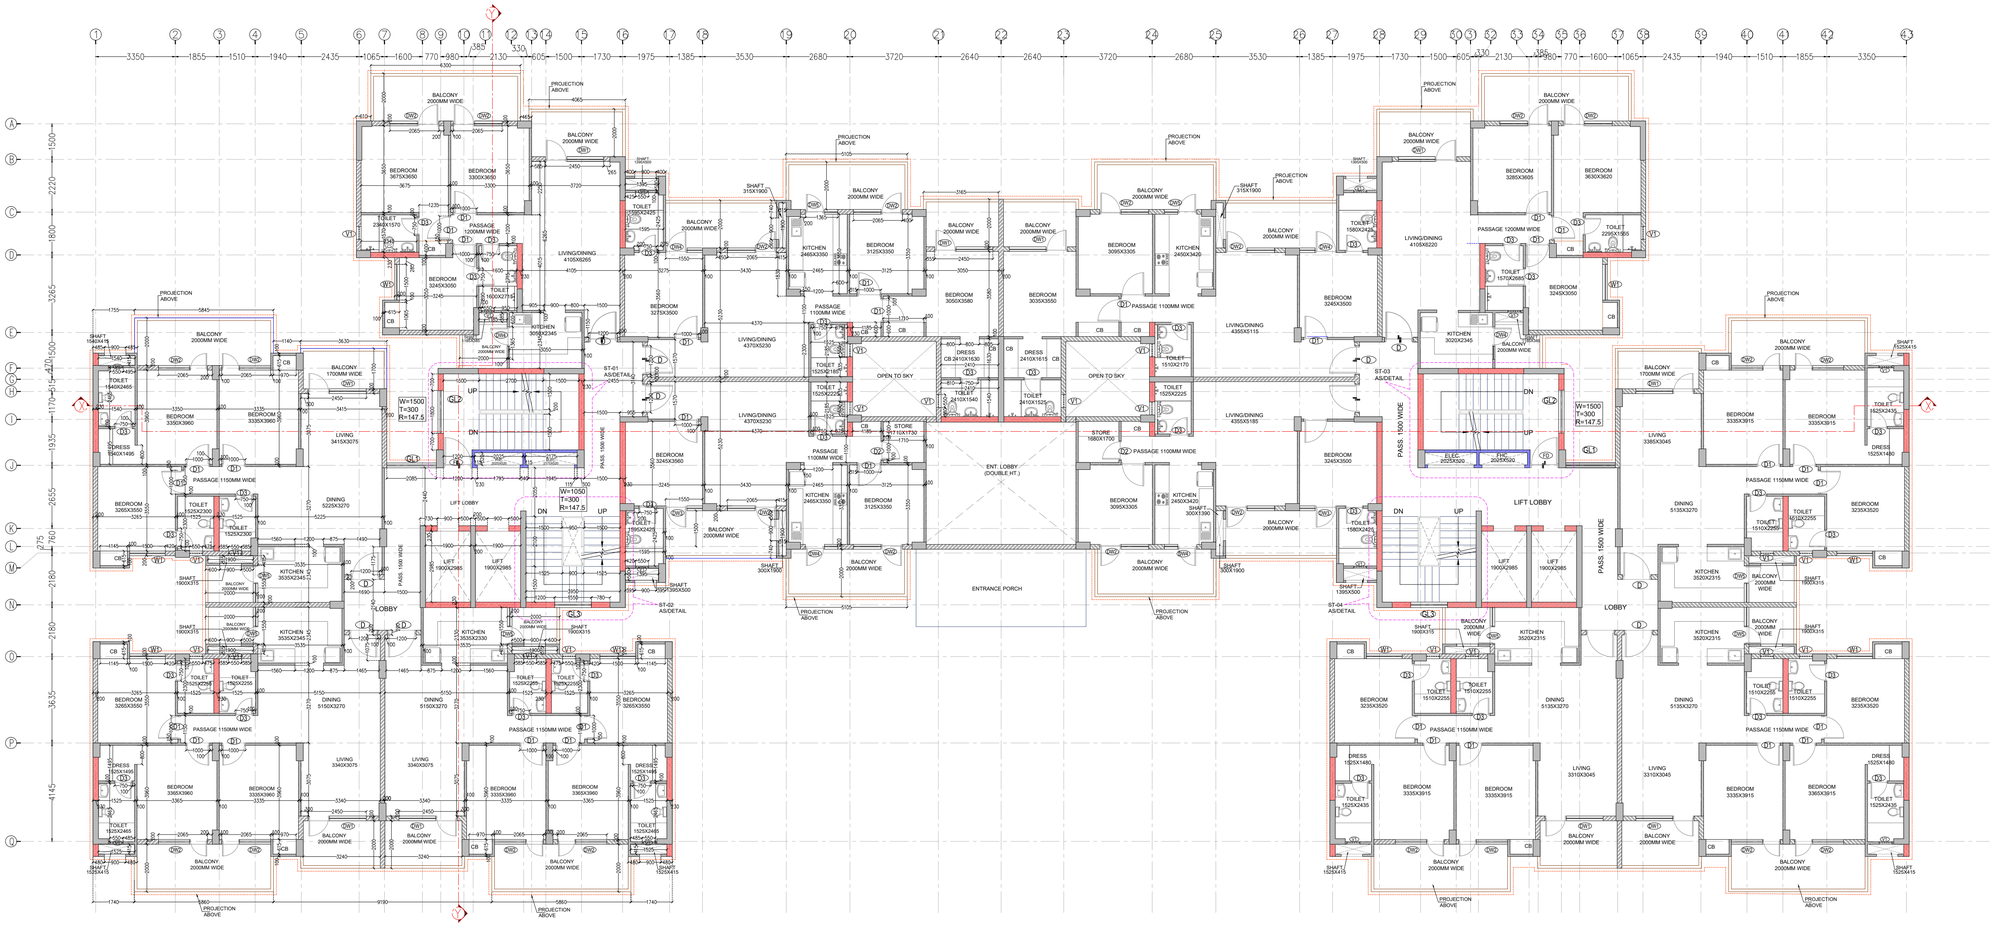


# FIRST FLOOR LVL PLAN

NOTES:

1. THIS DRAWING IS NOT TO BE SCALED. ONLY WRITTEN DIMENSIONS ARE TO BE FOLLOWED.
2. ALL DIMENSION SHALL BE CHECKED AT SITE BEFORE COMMENCEMENT OF WORK.
3. ANY DISCREPANCY MUST BE BROUGHT IN THE NOTICE OF ARCHITECT IMMEDIATELY.
4. THIS DWG. SHALL BE READ IN CONJUNCTION WITH STRUCTURE AND OTHER SERVICES DWG.

| S.NO. | DATE | REMARK |
|---|---|---|
| R1 | 11.09.25 | BALCONY DEPTH INCREASE D AS MENTIONED |

REVISIONS-:

**SCHEDULE OF OPENING**

| S. NO. | LEGEND | WIDTH MM | HEIGHT MM | CILL MM | LINTEL MM | REMARK |
|---|---|---|---|---|---|---|
| 01 | D | 1200 | 2400 | - | 2400 | MAIN DOOR |
| 02 | D1 | 1000 | 2200 | - | 2200 | BEDROOMS |
| 03 | D2 | 800 | 2200 | - | 2200 | STORE |
| 04 | D3 | 750 | 2200 | - | 2200 | TOILETS |
| 05 | FD | 1200 | 2200 | - | 2200 | FIRE DOOR |
| 08 | DW1 | 2450 | 2400 | 00/100 | 2400 | EXTERNAL DOOR |
| 09 | DW2 | 2065 | 2400 | 00/100 | 2400 | EXTERNAL DOOR |
| 10 | DW3 | 1550 | 2400 | 00/100 | 2400 | EXTERNAL DOOR |
| 11 | DW4 | 1365 | 2400 | 00/1050 | 2400 | KITCHEN |
| 12 | DW5 | 1550 | 2400 | 00/1050 | 2400 | KITCHEN |
| 13 | W1 | 1500 | 1500 | 900 | 2400 | BEDROOM |
| 14 | W2 | 1800 | 1550 | 900 | 2400 | STILT FLOOR |
| 15 | W3 | 1550 | 1550 | 900 | 2400 | STILT FLOOR |
| 16 | V1 | 550 | 1300 | 1100 | 2400 | TOILETS |
| 17 | GL | 2140 | 1500 | 900 | 2400 | LIFT LOBBY |
| 18 | GL1 | 2085 | 1500 | 900 | 2400 | LIFT LOBBY |
| 19 | GL2 | 1800 | 1500 | 900 | 2400 | STAIRCASE |
| 20 | GL3 | 1550 | 1500 | 900 | 2400 | STAIRCASE |

| | |
|---|---|
| | 200 MM BLOCK WORK |
| | 100 MM BLOCK WORK |
| | 230 MM BRICK WORK |
| | 115 MM BRICK WORK |

OMAXE ARCH. PLANNING DEPT.
ADVANCE COPY | TENDER COPY | GOOD FOR CONSTRUCTION
DATE | SIGN

DATE- September 11, 2025

OMAXE
TURNING DREAMS INTO REALITY

PROJECT TITLE-:

TOWER E, AANANDA PRAYAGRAJ

DRAWING TITLE-:

FIRST FLOOR PLAN

SCALE-NTS

DRAWING NO.

AANANDA/TOWER E/102