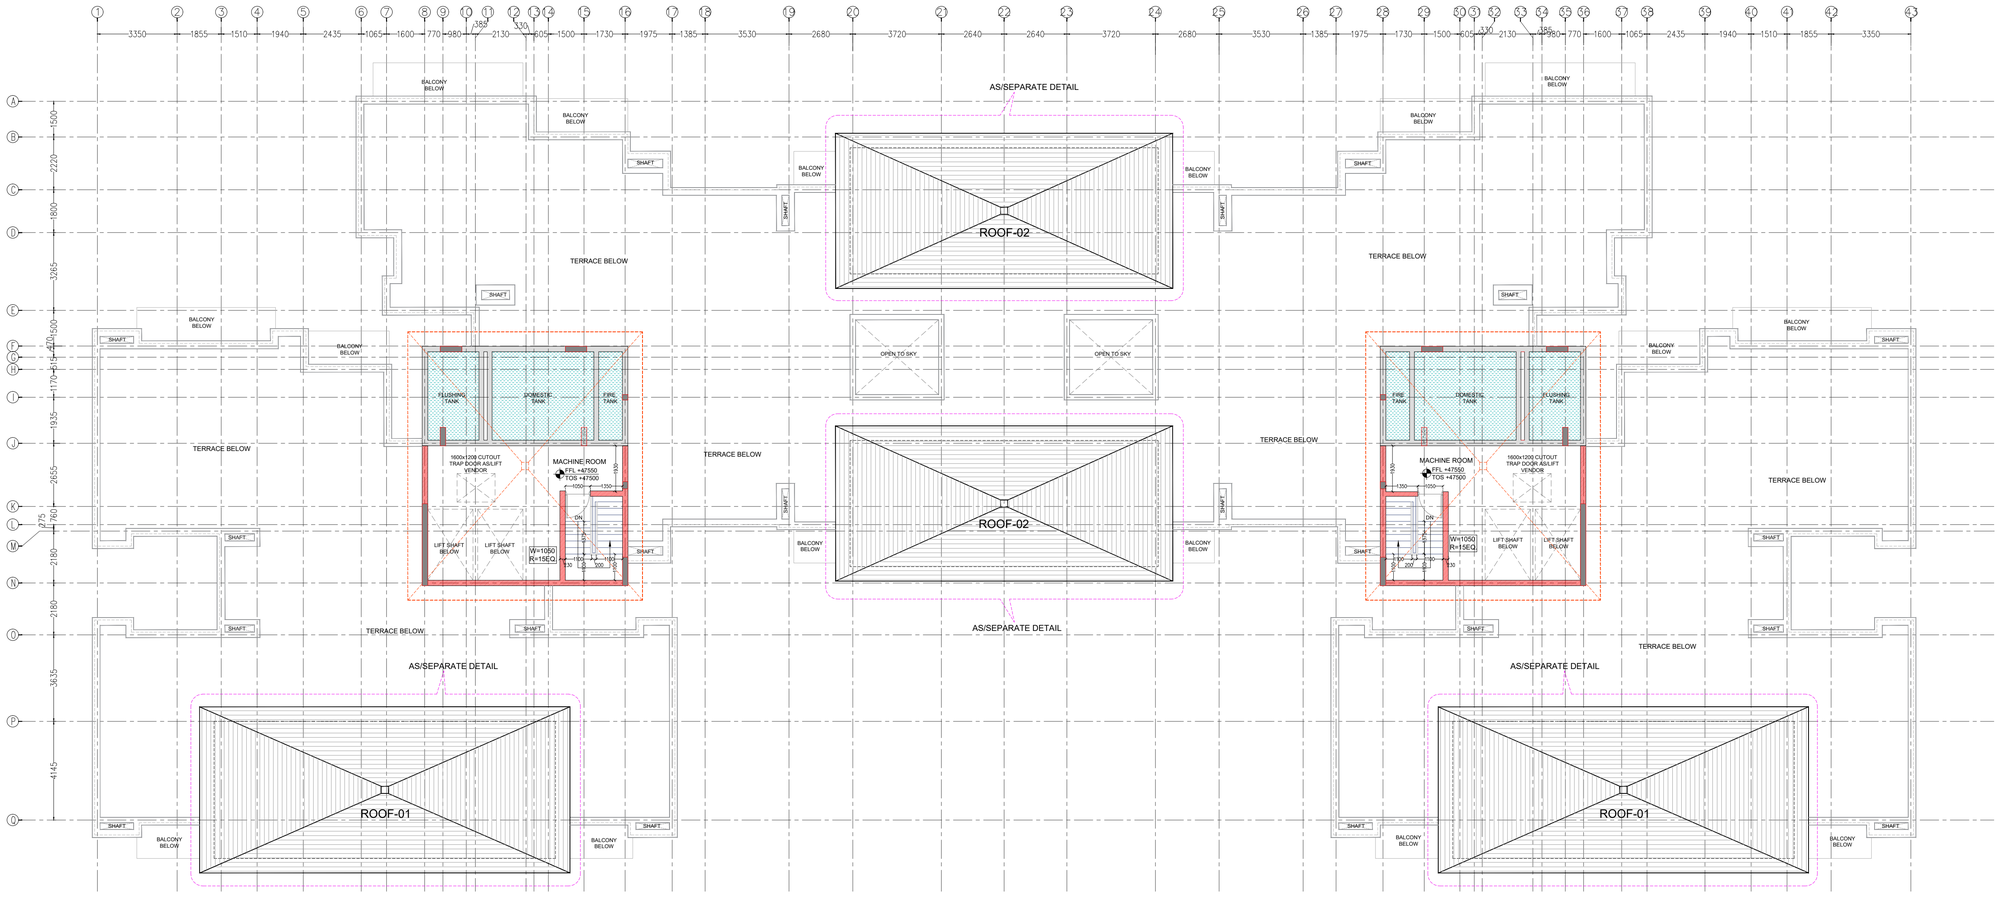

MACHINE ROOM LEVEL PLAN

NOTES:
1. THIS DRAWING IS NOT TO BE SCALED. ONLY WRITTEN DIMENSIONS ARE TO BE FOLLOWED.
2. ALL DIMENSION SHALL BE CHECKED AT SITE BEFORE COMMENCEMENT OF WORK.
3. ANY DISCREPANCY MUST BE BROUGHT IN THE NOTICE OF ARCHITECT IMMEDIATELY.
4. THIS DWG. SHALL BE READ IN CONJUNCTION WITH STRUCTURE AND OTHER SERVICES DWG.

S.NO.	DATE	REMARK

REVISIONS-:

	200 MM BLOCK WORK
	100 MM BLOCK WORK
	230 MM BRICK WORK
	115 MM BRICK WORK

OMAXE ARCH. PLANNING DEPT.
ADVANCE COPY | TENDER COPY | GOOD FOR CONSTRUCTION
DATE | SIGN

DATE- October 8, 2024

OMAXE
TURNING DREAMS INTO REALITY

PROJECT TITLE-:

TOWER E, AANANDA
PRAYAGRAJ

DRAWING TITLE-:

MACHINE ROOM LVL.
FLOOR PLAN

SCALE-NTS

DRAWING NO.

AANANDA/TOWER E/106