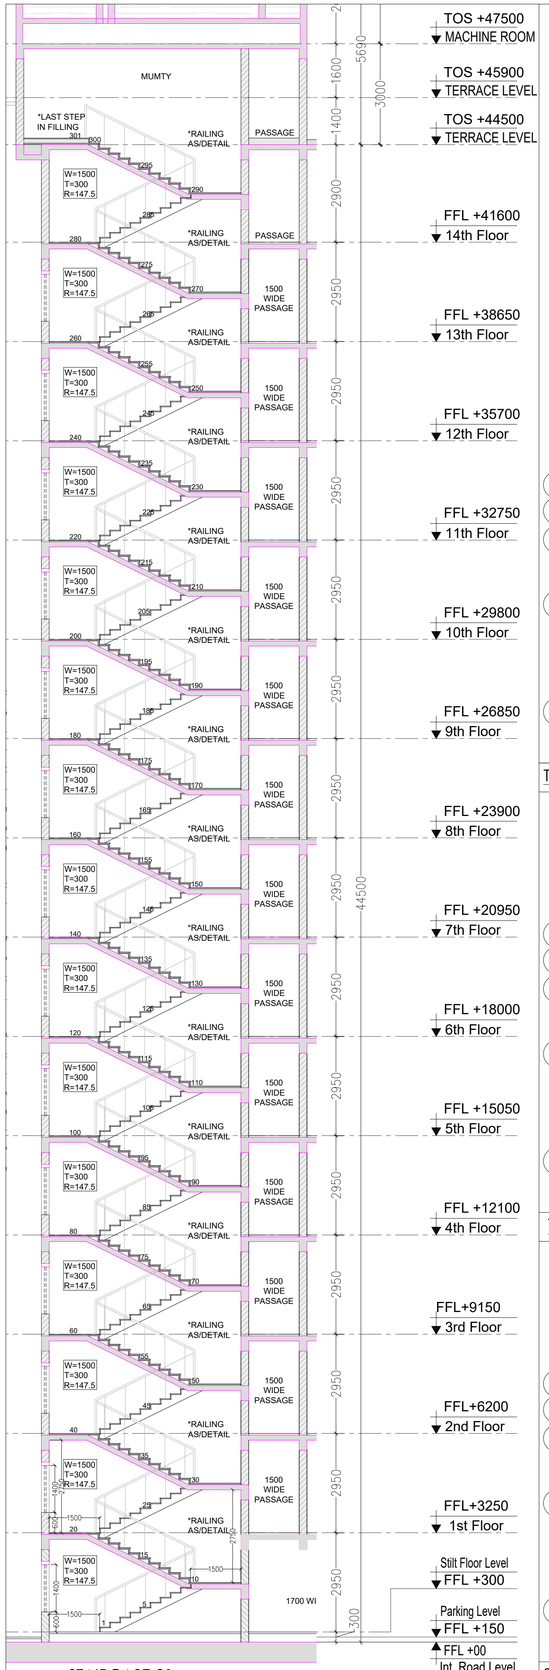

STAIRCASE-01

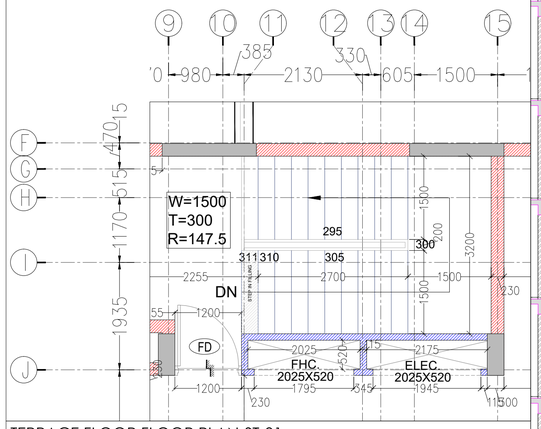

TERRACE FLOOR FLOOR PLAN-ST-01

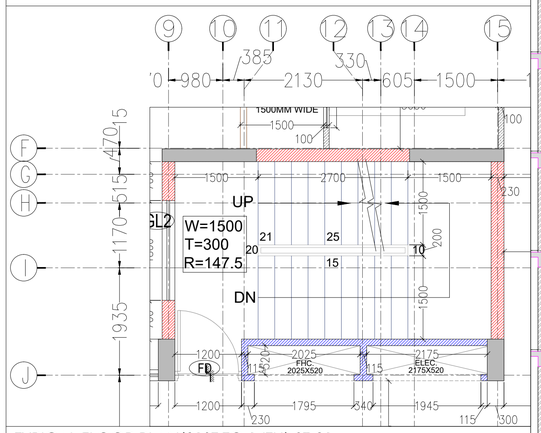

TYPICAL FLOOR PLAN(01ST TO 14TH)-ST-01

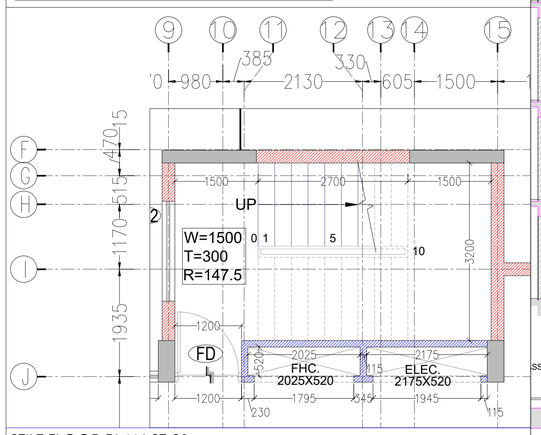

STILT FLOOR PLAN-ST-01

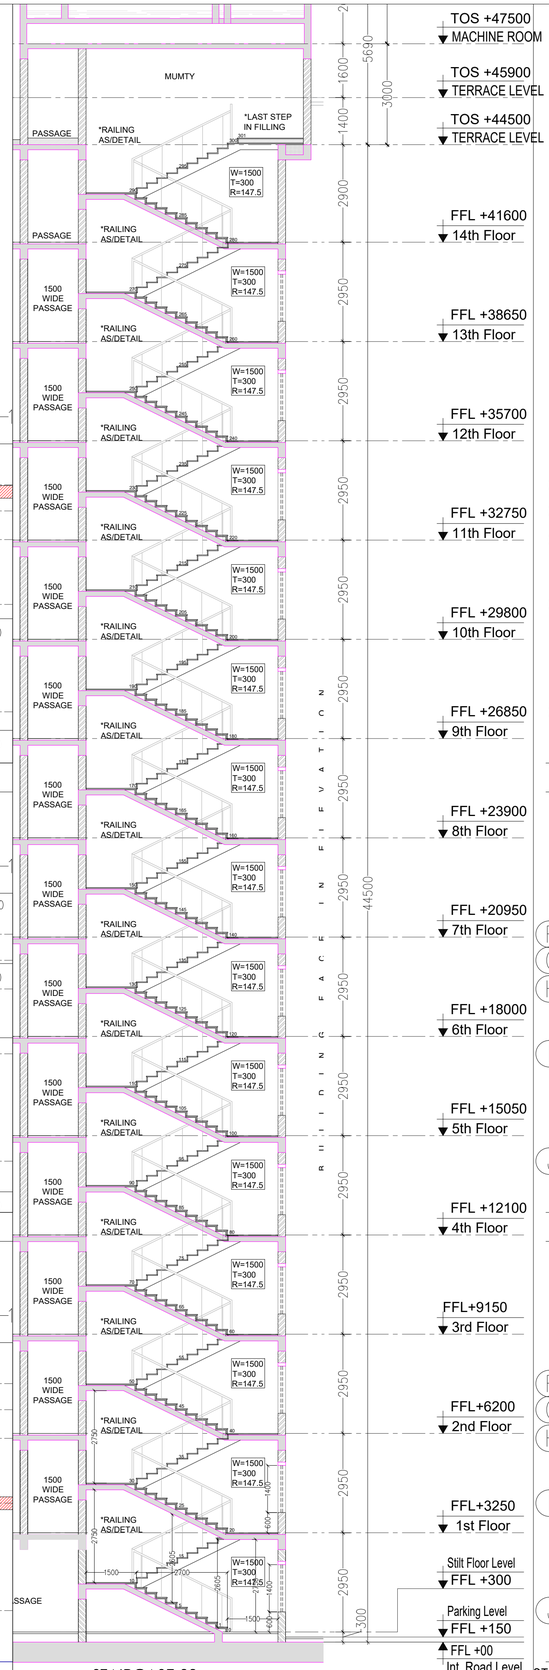

STAIRCASE-03

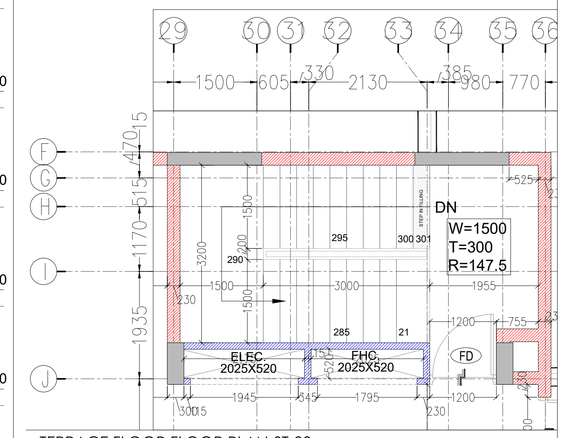

TERRACE FLOOR FLOOR PLAN-ST-03

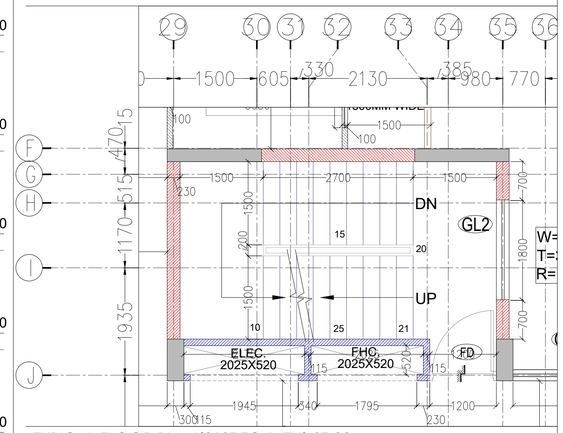

TYPICAL FLOOR PLAN(01ST TO 14TH)-ST-03

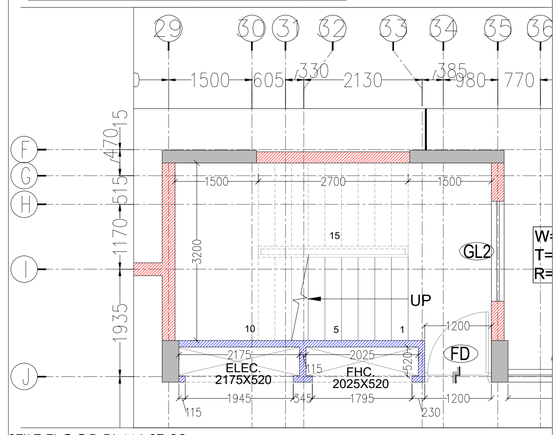

STILT FLOOR PLAN-ST-03

NOTES:
1. THIS DRAWING IS NOT TO BE SCALED. ONLY WRITTEN DIMENSIONS ARE TO BE FOLLOWED.
2. ALL DIMENSION SHALL BE CHECKED AT SITE BEFORE COMMENCEMENT OF WORK.
3. ANY DISCREPANCY MUST BE BROUGHT IN THE NOTICE OF ARCHITECT IMMEDIATELY.
4. THIS DWG. SHALL BE READ IN CONJUNCTION WITH STRUCTURE AND OTHER SERVICES DWG.

S.NO.	DATE	REMARK

REVISIONS-:

OMAXE ARCH. PLANNING DEPT.
ADVANCE COPY | TENDER COPY | GOOD FOR CONSTRUCTION
DATE | SIGN

DATE- October 8, 2024

OMAXE
TURNING DREAMS INTO REALITY

PROJECT TITLE-:

TOWER E, AANANDA PRAYAGRAJ

DRAWING TITLE-:

STAIRCASE 01 & 03

SCALE-NTS

DRAWING NO.

AANANDA/TOWER E/301