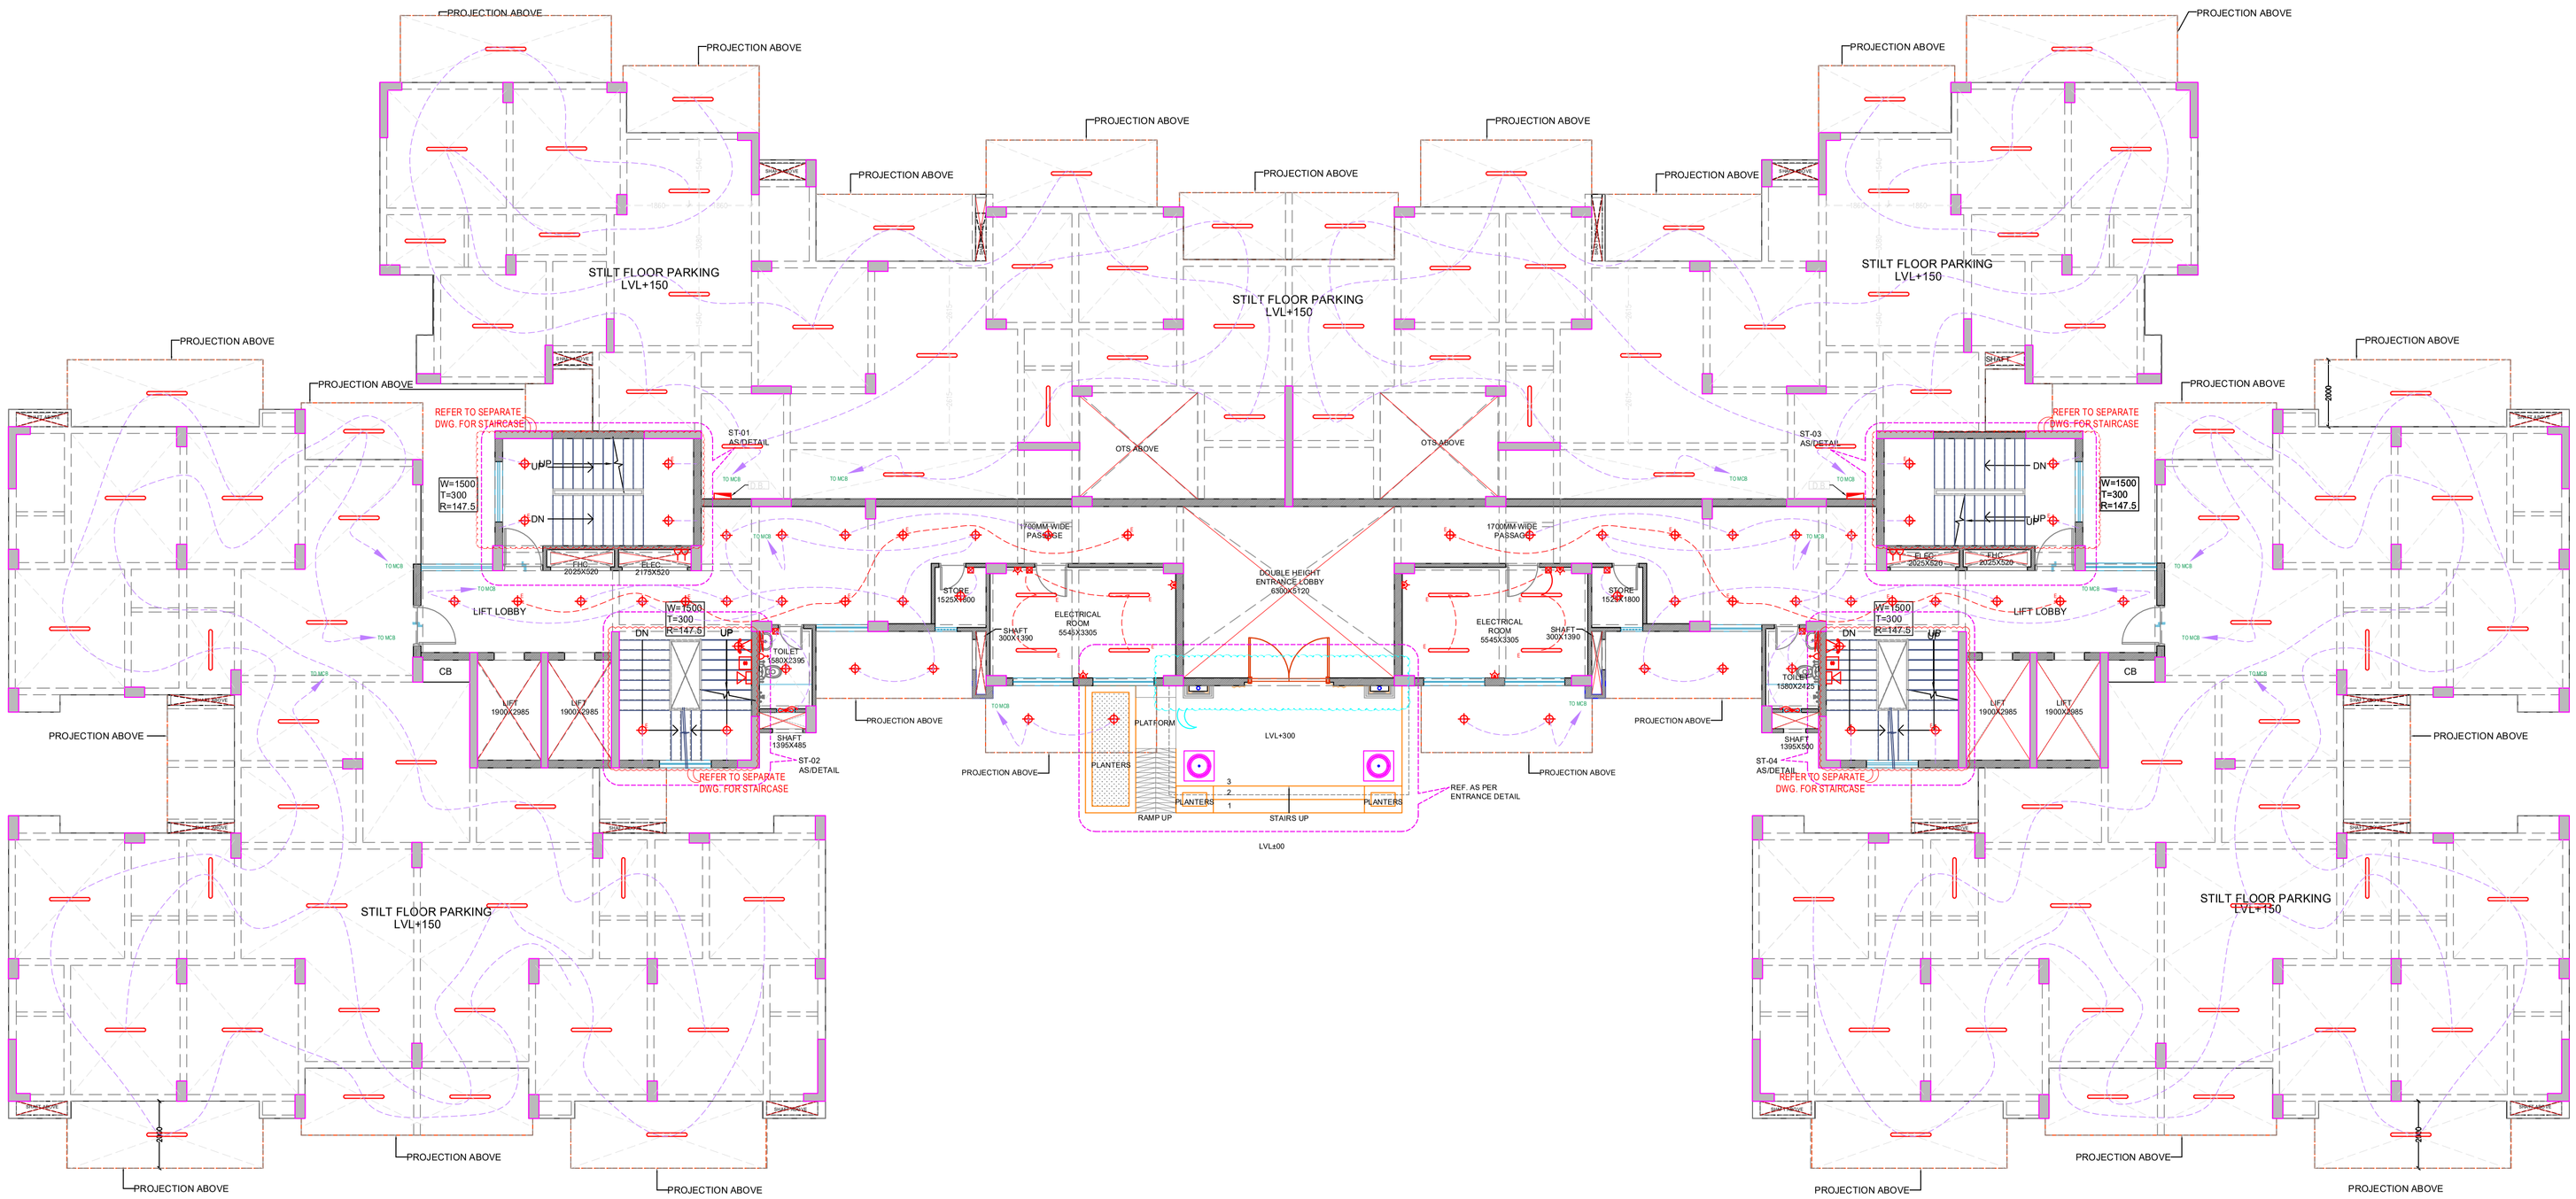

STILT FLOOR PLAN

NOTES:
1. THIS DRAWING IS NOT TO BE SCALED. ONLY WRITTEN DIMENSIONS ARE TO BE FOLLOWED.
2. ALL DIMENSION SHALL BE CHECKED AT SITE BEFORE COMMENCEMENT OF WORK.
3. ANY DISCREPANCY MUST BE BROUGHT IN THE NOTICE OF ARCHITECT IMMEDIATELY.
4. THIS DWG. SHALL BE READ IN CONJUNCTION WITH STRUCTURE AND OTHER SERVICES DWG.

LEGEND : (Electrical)

SYMBOL	DESCRIPTION	HEIGHT IN MM
	SWITCH BOARD	1050
	1 x 28 WATT TUBE LIGHT (SURFACE)	CEILING
	LIGHT POINT/ WALL BRACKET	2100
	CEILING LIGHT	CEILING
	EMERGENCY CEILING LIGHT	CEILING
	MIRROR LIGHT	2000
	EXHAUST FAN / CEILING ROSE	2150/2400
	BULK HEAD LIGHT	AS PER SITE
	6 AMP SOCKET WITH SWITCH	550
	6 AMP SOCKET WITH SWITCH	1050
	6 /16 AMP POWER POINT WITH SWITCH	550
	6 /16 AMP POWER POINT WITH SWITCH	1050
	DISTRIBUTION BOARD (BOTTOM)	1500
	LOOPING	
	SMOKE DETECTOR	CEILING
	MONITOR MODULE	AS PER SITE
	FIRE FIGHTING TELEPHONE JACK	550
	HOOTER	2150
	MANUAL CALL POINT	1050

NOTE: ELECTRICAL POINTS LOCATION & HEIGHT MAY BE CHANGE AS PER SITE CONDITION.

REV. NO.	DATE	DESCRIPTION
R0	28.11.2025	GFC

REVISIONS:

APPROVED BY

DEPARTMENT	STAMP
ARCHITECTURE	
STRUCTURE	
ELECTRICAL	
SERVICES	
LANDSCAPE	

PROJECT: TOWER E, AANANDA PRAYAGRAJ

CLIENT: OMAXE
TURNING DREAMS INTO REALITY

STAMP

DISCIPLINE: ELECTRICAL DRAWING

DRG. NO. AANANDA/TOWER-E/ EL/01

DRG. TITLE: **STILT FLOOR ELECTRICAL LAYOUT**

SCALE:	DATE (RO):	REVISION	REV. DATE :
NTS.	28.11.2025	R0	28.11.2025
DRAWN BY: L.C.	CHECKED BY: D.S.	STATUS: GOOD FOR CONSTRUCTION	

THIS DRAWING IS THE SOLE PROPERTY OF OMAXE LTD. USE OF THIS DRAWING FOR ANY PURPOSE OTHER THAN THAT MENTIONED TO BE DONE ONLY AFTER THEIR PRIOR APPROVAL.