SHEAR WALL SCHEDULE

MARK LEVEL

MARK LEVEL		SW1	SW2	SW3	SW4	SW5	SW6	SW7	SW8	SW9	SW10	SW11	SW12	SW13
ABOVE TO TERRACE LVL.	S.W.SIZE (TIES GROUP)					230X1700 G3					230X3445 G3	230X4065 G3	AS/SECTION G3	200X3445 G3
	VERTICAL REINF.					A = 8–20⌀ B = 8–16⌀ C = 8–12⌀					A = 8–16⌀ B = 8–12⌀ C = 26–10⌀	A = 8–16⌀ B = 8–12⌀ C = 32–10⌀	A = 8–16⌀ B =16–12⌀ C = 6–10⌀	A = 8–16⌀ B = 8–12⌀ C = 26–10⌀
	CONCRETE GRADE					M-30					M-30	M-30	M-30	M-30
	REFER SECTION					5B					10B	11C	12	13A
TERRACE LVL. TO 14TH FL00R LVL.	S.W.SIZE (TIES GROUP)	AS/SECTION G3	AS/SECTION G3	230X1000 G3	230X1150 G3	230X1700 G3	230X1185 G3	230X1855 G3	230X3600 G3	AS/SECTION G3	230X3445 G3	230X4065 G3	AS/SECTION G3	200X3445 G3
	VERTICAL REINF.	A = 8–16⌀ B =16–12⌀ C = 8–10⌀	A = 8–16⌀ B =16–12⌀ C =10–10⌀	A = 4–16⌀ B = 4–12⌀ C = 4–12⌀ D = 4–12⌀ E = 4–12⌀	A = 4–16⌀ B = 4–12⌀ C = 4–12⌀ D = 4–12⌀ E = 4–12⌀ F = 2–12⌀	A = 8–16⌀ B = 8–12⌀ C = 8–10⌀	A = 4–16⌀ B = 4–12⌀ C = 4–12⌀ D = 4–12⌀ E = 4–10⌀ F = 4–10⌀	A = 8–16⌀ B = 8–12⌀ C =10–10⌀	A = 8–16⌀ B = 8–12⌀ C =28–10⌀	A = 8–16⌀ B =16–12⌀ C =10–10⌀	A = 8–16⌀ B = 8–12⌀ C = 26–10⌀	A = 8–16⌀ B = 8–12⌀ C = 32–10⌀	A = 8–16⌀ B =16–12⌀ C = 6–10⌀	A = 8–16⌀ B = 8–12⌀ C = 26–10⌀
	CONCRETE GRADE	M-30	M-30	M-30	M-30	M-30	M-30	M-30	M-30	M-30	M-30	M-30	M-30	M-30
	REFER SECTION	1	2	3	4	5B	6	7B	8D	9	10B	11C	12	13A
14TH FL00R LVL. TO 13TH FL00R LVL.	S.W.SIZE (TIES GROUP)	AS/SECTION G3	AS/SECTION G3	230X1000 G3	230X1150 G3	230X1700 G3	230X1185 G3	230X1855 G3	230X3600 G3	AS/SECTION G3	230X3445 G3	230X4065 G3	AS/SECTION G3	200X3445 G3
	VERTICAL REINF.	A = 8–16⌀ B =16–12⌀ C = 8–10⌀	A = 8–16⌀ B =16–12⌀ C =10–10⌀	A = 4–16⌀ B = 4–12⌀ C = 4–12⌀ D = 4–12⌀ E = 4–12⌀	A = 4–16⌀ B = 4–12⌀ C = 4–12⌀ D = 4–12⌀ E = 4–12⌀ F = 2–12⌀	A = 8–16⌀ B = 8–12⌀ C = 8–10⌀	A = 4–16⌀ B = 4–12⌀ C = 4–12⌀ D = 4–12⌀ E = 4–10⌀ F = 4–10⌀	A = 8–16⌀ B = 8–12⌀ C =10–10⌀	A = 8–16⌀ B = 8–12⌀ C =28–10⌀	A = 8–16⌀ B =16–12⌀ C =10–10⌀	A = 8–16⌀ B = 8–12⌀ C = 26–10⌀	A = 8–16⌀ B = 8–12⌀ C = 32–10⌀	A = 8–16⌀ B =16–12⌀ C = 6–10⌀	A = 8–16⌀ B = 8–12⌀ C = 26–10⌀
	CONCRETE GRADE	M-30	M-30	M-30	M-30	M-30	M-30	M-30	M-30	M-30	M-30	M-30	M-30	M-30
	REFER SECTION	1	2	3	4	5B	6	7B	8D	9	10B	11C	12	13A
13TH FL00R LVL. TO 12TH FL00R LVL.	S.W.SIZE (TIES GROUP)	AS/SECTION G3	AS/SECTION G3	230X1000 G3	230X1150 G3	230X1700 G3	230X1185 G3	230X1855 G3	230X3600 G3	AS/SECTION G3	230X3445 G3	230X4065 G3	AS/SECTION G3	200X3445 G3
	VERTICAL REINF.	A = 8–16⌀ B =16–12⌀ C = 8–10⌀	A = 8–16⌀ B =16–12⌀ C =10–10⌀	A = 4–16⌀ B = 4–12⌀ C = 4–12⌀ D = 4–12⌀ E = 4–12⌀	A = 4–16⌀ B = 4–12⌀ C = 4–12⌀ D = 4–12⌀ E = 4–12⌀ F = 2–12⌀	A = 8–16⌀ B = 8–12⌀ C = 8–10⌀	A = 4–16⌀ B = 4–12⌀ C = 4–12⌀ D = 4–12⌀ E = 4–10⌀ F = 4–10⌀	A = 8–16⌀ B = 8–12⌀ C =10–10⌀	A = 8–16⌀ B = 8–12⌀ C =28–10⌀	A = 8–16⌀ B =16–12⌀ C =10–10⌀	A = 8–16⌀ B = 8–12⌀ C = 26–10⌀	A = 8–16⌀ B = 8–12⌀ C = 32–10⌀	A = 8–16⌀ B =16–12⌀ C = 6–10⌀	A = 8–16⌀ B = 8–12⌀ C = 26–10⌀
	CONCRETE GRADE	M-30	M-30	M-30	M-30	M-30	M-30	M-30	M-30	M-30	M-30	M-30	M-30	M-30
	REFER SECTION	1	2	3	4	5B	6	7B	8D	9	10B	11C	12	13A
12TH FL00R LVL. TO 11TH FL00R LVL.	S.W.SIZE (TIES GROUP)	AS/SECTION G3	AS/SECTION G3	230X1000 G3	230X1150 G3	230X1700 G3	230X1185 G3	230X1855 G3	230X3600 G3	AS/SECTION G3	230X3445 G3	230X4065 G3	AS/SECTION G3	200X3445 G3
	VERTICAL REINF.	A = 8–16⌀ B =16–12⌀ C = 8–10⌀	A = 8–16⌀ B =16–12⌀ C =10–10⌀	A = 4–16⌀ B = 4–12⌀ C = 4–12⌀ D = 4–12⌀ E = 4–12⌀	A = 4–16⌀ B = 4–12⌀ C = 4–12⌀ D = 4–12⌀ E = 4–12⌀ F = 2–12⌀	A = 8–16⌀ B = 8–12⌀ C = 8–10⌀	A = 4–16⌀ B = 4–12⌀ C = 4–12⌀ D = 4–12⌀ E = 4–10⌀ F = 4–10⌀	A = 8–16⌀ B = 8–12⌀ C =10–10⌀	A = 8–16⌀ B = 8–12⌀ C =28–10⌀	A = 8–16⌀ B =16–12⌀ C =10–10⌀	A = 8–16⌀ B = 8–12⌀ C = 26–10⌀	A = 8–16⌀ B = 8–12⌀ C = 32–10⌀	A = 8–16⌀ B =16–12⌀ C = 6–10⌀	A = 8–16⌀ B = 8–12⌀ C = 26–10⌀
	CONCRETE GRADE	M-30	M-30	M-30	M-30	M-30	M-30	M-30	M-30	M-30	M-30	M-30	M-30	M-30
	REFER SECTION	1	2	3	4	5B	6	7B	8D	9	10B	11C	12	13A
11TH FL00R LVL. TO 10TH FL00R LVL.	S.W.SIZE (TIES GROUP)	AS/SECTION G3	AS/SECTION G3	230X1000 G3	230X1150 G3	230X1700 G3	230X1185 G3	230X1855 G3	230X3600 G3	AS/SECTION G3	230X3445 G3	230X4065 G3	AS/SECTION G3	200X3445 G3
	VERTICAL REINF.	A = 8–16⌀ B =16–12⌀ C = 8–10⌀	A = 8–16⌀ B =16–12⌀ C =10–10⌀	A = 4–16⌀ B = 4–12⌀ C = 4–12⌀ D = 4–12⌀ E = 4–12⌀	A = 4–16⌀ B = 4–12⌀ C = 4–12⌀ D = 4–12⌀ E = 4–12⌀ F = 2–12⌀	A = 8–16⌀ B = 8–12⌀ C = 8–10⌀	A = 4–16⌀ B = 4–12⌀ C = 4–12⌀ D = 4–12⌀ E = 4–10⌀ F = 4–10⌀	A = 8–16⌀ B = 8–12⌀ C =10–10⌀	A = 8–16⌀ B = 8–12⌀ C =28–10⌀	A = 8–16⌀ B =16–12⌀ C =10–10⌀	A = 8–16⌀ B = 8–12⌀ C = 26–10⌀	A = 8–16⌀ B = 8–12⌀ C = 32–10⌀	A = 8–16⌀ B =16–12⌀ C = 6–10⌀	A = 8–16⌀ B = 8–12⌀ C = 26–10⌀
	CONCRETE GRADE	M-30	M-30	M-30	M-30	M-30	M-30	M-30	M-30	M-30	M-30	M-30	M-30	M-30
	REFER SECTION	1	2	3	4	5B	6	7B	8D	9	10B	11C	12	13A
10TH FL00R LVL. TO 9TH FL00R LVL.	S.W.SIZE (TIES GROUP)	AS/SECTION G3	AS/SECTION G3	230X1000 G3	230X1150 G3	230X1700 G3	230X1185 G3	230X1855 G3	230X3600 G3	AS/SECTION G3	230X3445 G3	230X4065 G3	AS/SECTION G3	200X3445 G3
	VERTICAL REINF.	A = 8–16⌀ B =16–12⌀ C = 8–10⌀	A = 8–16⌀ B =16–12⌀ C =10–10⌀	A = 4–16⌀ B = 4–12⌀ C = 4–12⌀ D = 4–12⌀ E = 4–12⌀	A = 4–16⌀ B = 4–12⌀ C = 4–12⌀ D = 4–12⌀ E = 4–12⌀ F = 2–12⌀	A = 8–16⌀ B = 8–12⌀ C = 8–10⌀	A = 4–16⌀ B = 4–12⌀ C = 4–12⌀ D = 4–12⌀ E = 4–10⌀ F = 4–10⌀	A = 8–16⌀ B = 8–12⌀ C =10–10⌀	A = 8–16⌀ B = 8–12⌀ C =28–10⌀	A = 8–16⌀ B =16–12⌀ C =10–10⌀	A = 8–16⌀ B = 8–12⌀ C = 26–10⌀	A = 8–16⌀ B = 8–12⌀ C = 32–10⌀	A = 8–16⌀ B =16–12⌀ C = 6–10⌀	A = 8–16⌀ B = 8–12⌀ C = 26–10⌀
	CONCRETE GRADE	M-30	M-30	M-30	M-30	M-30	M-30	M-30	M-30	M-30	M-30	M-30	M-30	M-30
	REFER SECTION	1	2	3	4	5B	6	7B	8D	9	10B	11B	12	13A
9TH FL00R LVL. TO 8TH FL00R LVL.	S.W.SIZE (TIES GROUP)	AS/SECTION G3	AS/SECTION G3	230X1000 G3	230X1150 G3	230X1700 G3	230X1185 G3	230X1855 G3	230X3600 G3	AS/SECTION G3	230X3445 G3	230X4065 G3	AS/SECTION G3	200X3445 G3
	VERTICAL REINF.	A = 8–16⌀ B =16–12⌀ C = 8–10⌀	A = 8–16⌀ B =16–12⌀ C =10–10⌀	A = 4–16⌀ B = 4–12⌀ C = 4–12⌀ D = 4–12⌀ E = 4–12⌀	A = 4–16⌀ B = 4–12⌀ C = 4–12⌀ D = 4–12⌀ E = 4–12⌀ F = 2–12⌀	A = 8–16⌀ B = 8–12⌀ C = 8–10⌀	A = 4–16⌀ B = 4–12⌀ C = 4–12⌀ D = 4–12⌀ E = 4–10⌀ F = 4–10⌀	A = 8–16⌀ B = 8–12⌀ C =10–10⌀	A = 8–16⌀ B = 8–12⌀ C = 4–12⌀ D =26–10⌀	A = 8–16⌀ B =16–12⌀ C =10–10⌀	A = 8–16⌀ B = 8–12⌀ C = 26–10⌀	A = 8–16⌀ B = 8–12⌀ C = 4–12⌀ D =30–10⌀	A = 8–16⌀ B =16–12⌀ C = 6–10⌀	A = 8–16⌀ B = 8–12⌀ C = 26–10⌀
	CONCRETE GRADE	M-30	M-30	M-30	M-30	M-30	M-30	M-30	M-30	M-30	M-30	M-30	M-30	M-30
	REFER SECTION	1	2	3	4	5B	6	7B	8C	9	10B	11B	12	13A
8TH FL00R LVL. TO 7TH FL00R LVL.	S.W.SIZE (TIES GROUP)	AS/SECTION G3	AS/SECTION G3	230X1000 G3	230X1150 G3	230X1700 G3	230X1185 G3	230X1855 G3	230X3600 G3	AS/SECTION G3	230X3445 G3	230X4065 G3	AS/SECTION G3	200X3445 G3
	VERTICAL REINF.	A = 8–16⌀ B =16–12⌀ C = 8–10⌀	A = 8–16⌀ B =16–12⌀ C =10–10⌀	A = 4–16⌀ B = 4–12⌀ C = 4–12⌀ D = 4–12⌀ E = 4–12⌀	A = 4–16⌀ B = 4–12⌀ C = 4–12⌀ D = 4–12⌀ E = 4–12⌀ F = 2–12⌀	A = 8–16⌀ B = 8–12⌀ C = 8–10⌀	A = 4–16⌀ B = 4–12⌀ C = 4–12⌀ D = 4–12⌀ E = 4–10⌀ F = 4–10⌀	A = 8–16⌀ B = 8–12⌀ C =10–10⌀	A = 8–16⌀ B = 8–12⌀ C = 4–12⌀ D =26–10⌀	A = 8–16⌀ B =16–12⌀ C =10–10⌀	A = 8–16⌀ B = 8–12⌀ C = 26–10⌀	A = 8–16⌀ B = 8–12⌀ C = 4–12⌀ D =30–10⌀	A = 8–16⌀ B =16–12⌀ C = 6–10⌀	A = 8–16⌀ B = 8–12⌀ C = 26–10⌀
	CONCRETE GRADE	M-30	M-30	M-30	M-30	M-30	M-30	M-30	M-30	M-30	M-30	M-30	M-30	M-30
	REFER SECTION	1	2	3	4	5B	6	7B	8C	9	10B	11B	12	13A
7TH FL00R LVL. TO 6TH FL00R LVL.	S.W.SIZE (TIES GROUP)	AS/SECTION G3	AS/SECTION G3	230X1000 G3	230X1150 G3	230X1700 G3	230X1185 G3	230X1855 G3	230X3600 G3	AS/SECTION G3	230X3445 G3	230X4065 G3	AS/SECTION G3	200X3445 G3
	VERTICAL REINF.	A = 8–16⌀ B =16–12⌀ C = 8–10⌀	A = 8–16⌀ B =16–12⌀ C =10–10⌀	A = 4–16⌀ B = 4–12⌀ C = 4–12⌀ D = 4–12⌀ E = 4–12⌀	A = 4–16⌀ B = 4–12⌀ C = 4–12⌀ D = 4–12⌀ E = 4–12⌀ F = 2–12⌀	A = 8–16⌀ B = 8–12⌀ C = 8–10⌀	A = 4–16⌀ B = 4–12⌀ C = 4–12⌀ D = 4–12⌀ E = 4–10⌀ F = 4–10⌀	A = 8–16⌀ B = 8–12⌀ C =10–10⌀	A = 8–16⌀ B = 8–12⌀ C = 8–12⌀ D = 4–12⌀ E =22–10⌀	A = 8–16⌀ B =16–12⌀ C =10–10⌀	A = 8–16⌀ B = 8–12⌀ C = 26–10⌀	A = 8–16⌀ B = 8–12⌀ C = 4–12⌀ D =30–10⌀	A = 8–16⌀ B =16–12⌀ C = 6–10⌀	A = 8–16⌀ B = 8–12⌀ C = 26–10⌀
	CONCRETE GRADE	M-30	M-30	M-30	M-30	M-30	M-30	M-30	M-30	M-30	M-30	M-30	M-30	M-30
	REFER SECTION	1	2	3	4	5B	6	7B	8B	9	10B	11B	12	13A
6TH FL00R LVL. TO 5TH FL00R LVL.	S.W.SIZE (TIES GROUP)	AS/SECTION G3	AS/SECTION G3	230X1000 G3	230X1150 G3	230X1700 G3	230X1185 G3	230X1855 G3	230X3600 G3	AS/SECTION G3	230X3445 G3	230X4065 G3	AS/SECTION G3	200X3445 G3
	VERTICAL REINF.	A = 8–16⌀ B =16–12⌀ C = 8–10⌀	A = 8–16⌀ B =16–12⌀ C =10–10⌀	A = 4–16⌀ B = 4–12⌀ C = 4–12⌀ D = 4–12⌀ E = 4–12⌀	A = 4–16⌀ B = 4–12⌀ C = 4–12⌀ D = 4–12⌀ E = 4–12⌀ F = 2–12⌀	A = 8–16⌀ B = 8–12⌀ C = 8–10⌀	A = 4–16⌀ B = 4–12⌀ C = 4–12⌀ D = 4–12⌀ E = 4–10⌀ F = 4–10⌀	A = 8–16⌀ B = 8–12⌀ C =10–10⌀	A = 8–16⌀ B = 8–12⌀ C = 8–12⌀ D = 4–12⌀ E =22–10⌀	A = 8–16⌀ B =16–12⌀ C =10–10⌀	A = 8–16⌀ B = 8–12⌀ C = 26–10⌀	A = 8–16⌀ B = 8–12⌀ C = 8–12⌀ D = 4–12⌀ E =26–10⌀	A = 8–16⌀ B =16–12⌀ C = 6–10⌀	A = 8–16⌀ B = 8–12⌀ C = 26–10⌀
	CONCRETE GRADE	M-30	M-30	M-30	M-30	M-30	M-30	M-30	M-30	M-30	M-30	M-30	M-30	M-30
	REFER SECTION	1	2	3	4	5B	6	7B	8B	9	10B	11A	12	13A
5TH FL00R LVL. TO 4TH FL00R LVL.	S.W.SIZE (TIES GROUP)	AS/SECTION G3	AS/SECTION G3	230X1000 G3	230X1150 G3	230X1700 G3	230X1185 G3	230X1855 G3	230X3600 G3	AS/SECTION G3	230X3445 G3	230X4065 G3	AS/SECTION G3	200X3445 G3
	VERTICAL REINF.	A = 8–16⌀ B =16–12⌀ C = 8–10⌀	A = 8–16⌀ B =16–12⌀ C =10–10⌀	A = 4–16⌀ B = 4–12⌀ C = 4–12⌀ D = 4–12⌀ E = 4–12⌀	A = 4–16⌀ B = 4–12⌀ C = 4–12⌀ D = 4–12⌀ E = 4–12⌀ F = 2–12⌀	A = 8–16⌀ B = 8–12⌀ C = 8–10⌀	A = 4–16⌀ B = 4–12⌀ C = 4–12⌀ D = 4–12⌀ E = 4–10⌀ F = 4–10⌀	A = 8–16⌀ B = 8–12⌀ C =10–10⌀	A = 8–16⌀ B = 8–12⌀ C = 8–12⌀ D = 4–12⌀ E =22–10⌀	A = 8–16⌀ B =16–12⌀ C =10–10⌀	A = 8–16⌀ B = 8–12⌀ C = 4–12⌀ D =24–10⌀	A = 8–16⌀ B = 8–12⌀ C = 8–12⌀ D = 4–12⌀ E =26–10⌀	A = 8–16⌀ B =16–12⌀ C = 6–10⌀	A = 8–16⌀ B = 8–12⌀ C = 26–10⌀
	CONCRETE GRADE	M-35	M-35	M-35	M-35	M-35	M-35	M-35	M-35	M-35	M-35	M-35	M-35	M-35
	REFER SECTION	1	2	3	4	5B	6	7B	8B	9	10A	11A	12	13A
4TH FL00R LVL. TO 3RD FL00R LVL.	S.W.SIZE (TIES GROUP)	AS/SECTION G3	AS/SECTION G3	230X1000 G3	230X1150 G3	230X1700 G3	230X1185 G3	230X1855 G3	230X3600 G3	AS/SECTION G3	230X3445 G3	230X4065 G3	AS/SECTION G3	200X3445 G3
	VERTICAL REINF.	A = 8–16⌀ B =16–12⌀ C = 8–10⌀	A = 8–16⌀ B =16–12⌀ C =10–10⌀	A = 4–16⌀ B = 4–12⌀ C = 4–12⌀ D = 4–12⌀ E = 4–12⌀	A = 4–16⌀ B = 4–12⌀ C = 4–12⌀ D = 4–12⌀ E = 4–12⌀ F = 2–12⌀	A = 8–16⌀ B = 8–12⌀ C = 8–10⌀	A = 4–16⌀ B = 4–12⌀ C = 4–12⌀ D = 4–12⌀ E = 4–10⌀ F = 4–10⌀	A = 8–16⌀ B = 8–12⌀ C =10–10⌀	A = 8–16⌀ B = 8–12⌀ C = 8–12⌀ D = 4–12⌀ E =22–10⌀	A = 8–16⌀ B =16–12⌀ C =10–10⌀	A = 8–16⌀ B = 8–12⌀ C = 4–12⌀ D =24–10⌀	A = 8–16⌀ B = 8–12⌀ C = 8–12⌀ D = 4–12⌀ E =26–10⌀	A = 8–16⌀ B =16–12⌀ C = 6–10⌀	A = 8–16⌀ B = 8–12⌀ C = 26–10⌀
	CONCRETE GRADE	M-35	M-35	M-35	M-35	M-35	M-35	M-35	M-35	M-35	M-35	M-35	M-35	M-35
	REFER SECTION	1	2	3	4	5B	6	7B	8B	9	10A	11A	12	13A
3RD FL00R LVL. TO 2ND FL00R LVL.	S.W.SIZE (TIES GROUP)	AS/SECTION G3	AS/SECTION G3	230X1000 G3	230X1150 G3	230X1700 G3	230X1185 G3	230X1855 G3	230X3600 G3	AS/SECTION G3	230X3445 G3	230X4065 G3	AS/SECTION G3	200X3445 G3
	VERTICAL REINF.	A = 8–16⌀ B =16–12⌀ C = 8–10⌀	A = 8–16⌀ B =16–12⌀ C =10–10⌀	A = 4–16⌀ B = 4–12⌀ C = 4–12⌀ D = 4–12⌀ E = 4–12⌀	A = 4–16⌀ B = 4–12⌀ C = 4–12⌀ D = 4–12⌀ E = 4–12⌀ F = 2–12⌀	A = 8–16⌀ B = 8–12⌀ C = 8–10⌀	A = 4–16⌀ B = 4–12⌀ C = 4–12⌀ D = 4–12⌀ E = 4–12⌀ F = 4–12⌀	A = 8–16⌀ B = 8–12⌀ C =10–10⌀	A = 8–16⌀ B = 8–12⌀ C = 8–12⌀ D = 8–12⌀ E = 8–12⌀ F =16–10⌀	A = 8–16⌀ B =16–12⌀ C =10–10⌀	A = 8–16⌀ B = 8–12⌀ C = 4–12⌀ D =24–10⌀	A = 8–16⌀ B = 8–12⌀ C = 8–12⌀ D = 4–12⌀ E =26–10⌀	A = 8–16⌀ B =16–12⌀ C = 6–10⌀	A = 8–16⌀ B = 8–12⌀ C = 26–10⌀
	CONCRETE GRADE	M-35	M-35	M-35	M-35	M-35	M-35	M-35	M-35	M-35	M-35	M-35	M-35	M-35
	REFER SECTION	1	2	3	4	5B	6	7B	8A	9	10A	11A	12	13A
2ND FL00R LVL. TO 1ST FL00R LVL.	S.W.SIZE (TIES GROUP)	AS/SECTION G3	AS/SECTION G3	230X1000 G3	230X1150 G3	230X1700 G3	230X1185 G3	230X1855 G3	230X3600 G3	AS/SECTION G3	230X3445 G3	230X4065 G3	AS/SECTION G3	200X3445 G3
	VERTICAL REINF.	A = 8–16⌀ B =16–12⌀ C = 8–10⌀	A = 8–16⌀ B =16–12⌀ C =10–10⌀	A = 4–16⌀ B = 4–12⌀ C = 4–12⌀ D = 4–12⌀ E = 4–12⌀	A = 4–16⌀ B = 4–12⌀ C = 4–12⌀ D = 4–12⌀ E = 4–12⌀ F = 2–12⌀	A = 8–16⌀ B = 8–12⌀ D = 4–12⌀	A = 4–16⌀ B = 4–12⌀ C = 4–12⌀ D = 4–12⌀ E = 4–12⌀ F = 4–12⌀	A = 8–16⌀ B = 8–12⌀ D = 6–12⌀	A = 8–16⌀ B = 8–16⌀ C = 8–16⌀ D = 8–16⌀ E = 8–16⌀ F = 16–12⌀	A = 8–16⌀ B =16–12⌀ C =10–10⌀	A = 8–16⌀ B = 8–12⌀ C = 8–12⌀ D = 4–12⌀ E =20–10⌀	A = 8–16⌀ B = 8–12⌀ C = 8–12⌀ D = 8–12⌀ E = 8–12⌀ F =20–10⌀	A = 8–16⌀ B =16–12⌀ C = 6–10⌀	A = 8–16⌀ B = 8–12⌀ C = 8–12⌀ D =22–10⌀
	CONCRETE GRADE	M-35	M-35	M-35	M-35	M-35	M-35	M-35	M-35	M-35	M-35	M-35	M-35	M-35
	REFER SECTION	1	2	3	4	5A	6	7B	8A	9	10	11	12	13
1ST FL00R LVL. TO GROUND FLOOR LVL.	S.W.SIZE (TIES GROUP)	AS/SECTION G3	AS/SECTION G3	230X1000 G3	230X1150 G3	230X1700 G3	230X1185 G3	230X1855 G3	230X3600 G3	AS/SECTION G3	230X3445 G3	230X4065 G3	AS/SECTION G3	200X3445 G3
	VERTICAL REINF.	A = 8–16⌀ B =16–12⌀ C = 8–10⌀	A = 8–16⌀ B =16–12⌀ C =10–10⌀	A = 4–16⌀ B = 4–12⌀ C = 4–12⌀ D = 4–12⌀ E = 4–12⌀	A = 4–16⌀ B = 4–12⌀ C = 4–12⌀ D = 4–12⌀ E = 4–12⌀ F = 2–12⌀	A = 8–16⌀ B = 8–16⌀ C = 8–16⌀ D = 4–12⌀	A = 4–16⌀ B = 4–16⌀ C = 4–16⌀ D = 4–12⌀ E = 4–12⌀ F = 4–12⌀	A = 4–16⌀ B = 4–16⌀ C = 4–16⌀ D = 4–16⌀ E = 4–16⌀ F = 4–16⌀ H = 6–12⌀	A = 8–16⌀ B = 8–16⌀ C = 8–16⌀ D = 8–16⌀ E = 8–16⌀ F = 8–12⌀ G =12–12⌀	A = 8–16⌀ B =16–12⌀ C =10–10⌀	A = 8–16⌀ B = 8–12⌀ C = 8–12⌀ D = 4–12⌀ E =20–10⌀	A = 8–16⌀ B = 8–16⌀ C = 8–12⌀ D = 8–12⌀ E = 8–12⌀ F =20–10⌀	A = 8–16⌀ B =16–12⌀ C = 6–10⌀	A = 8–16⌀ B = 8–12⌀ C = 8–12⌀ D =22–10⌀
	CONCRETE GRADE	M-35	M-35	M-35	M-35	M-35	M-35	M-35	M-35	M-35	M-35	M-35	M-35	M-35
	REFER SECTION	1	2	3	4	5A	6	7A	8	9	10	11	12	13
GROUND FLOOR LVL. TO FOUNDATION LVL.	S.W.SIZE (TIES GROUP)	AS/SECTION G3	AS/SECTION G3	230X1000 G3	230X1150 G3	230X1700 G3	230X1185 G3	230X1855 G3	230X3600 G3	AS/SECTION G3	230X3445 G3	230X4065 G3	AS/SECTION G3	200X3445 G3
	VERTICAL REINF.	A = 8–16⌀ B =16–12⌀ C = 8–10⌀	A = 8–16⌀ B =16–12⌀ C =10–10⌀	A = 4–16⌀ B = 4–12⌀ C = 4–12⌀ D = 4–12⌀ E = 4–12⌀	A = 4–16⌀ B = 4–12⌀ C = 4–12⌀ D = 4–12⌀ E = 4–12⌀ F = 2–12⌀	A = 4–20⌀ B = 4–20⌀ C = 4–20⌀ D = 4–16⌀ E = 4–16⌀ F = 8–16⌀ G = 6–16⌀	A = 4–16⌀ B = 4–16⌀ C = 4–16⌀ D = 4–12⌀ E = 4–12⌀ F = 4–12⌀	A = 4–16⌀ B = 4–16⌀ C = 4–16⌀ D = 4–16⌀ E = 4–16⌀ F = 4–16⌀ G = 4–16⌀ H = 8–16⌀	A = 8–16⌀ B = 8–16⌀ C = 8–16⌀ D = 8–16⌀ E = 8–16⌀ F = 8–16⌀ G =12–12⌀	A = 8–16⌀ B =16–12⌀ C =10–10⌀	A = 8–16⌀ B = 8–16⌀ C = 8–12⌀ D = 4–12⌀ E =20–12⌀	A = 8–16⌀ B = 8–16⌀ C = 8–12⌀ D = 8–12⌀ E = 8–12⌀ F =20–10⌀	A = 8–16⌀ B =16–12⌀ C = 6–10⌀	A = 8–16⌀ B = 8–12⌀ C = 8–12⌀ D =22–10⌀
	CONCRETE GRADE	M-35	M-35	M-35	M-35	M-35	M-35	M-35	M-35	M-35	M-35	M-35	M-35	M-35
	REFER SECTION	1	2	3	4	5	6	7	8	9	10	11	12	13
REMARK	DESCRIPTION	SW1	SW2	SW3	SW4	SW5	SW6	SW7	SW8	SW9	SW10	SW11	SW12	SW13

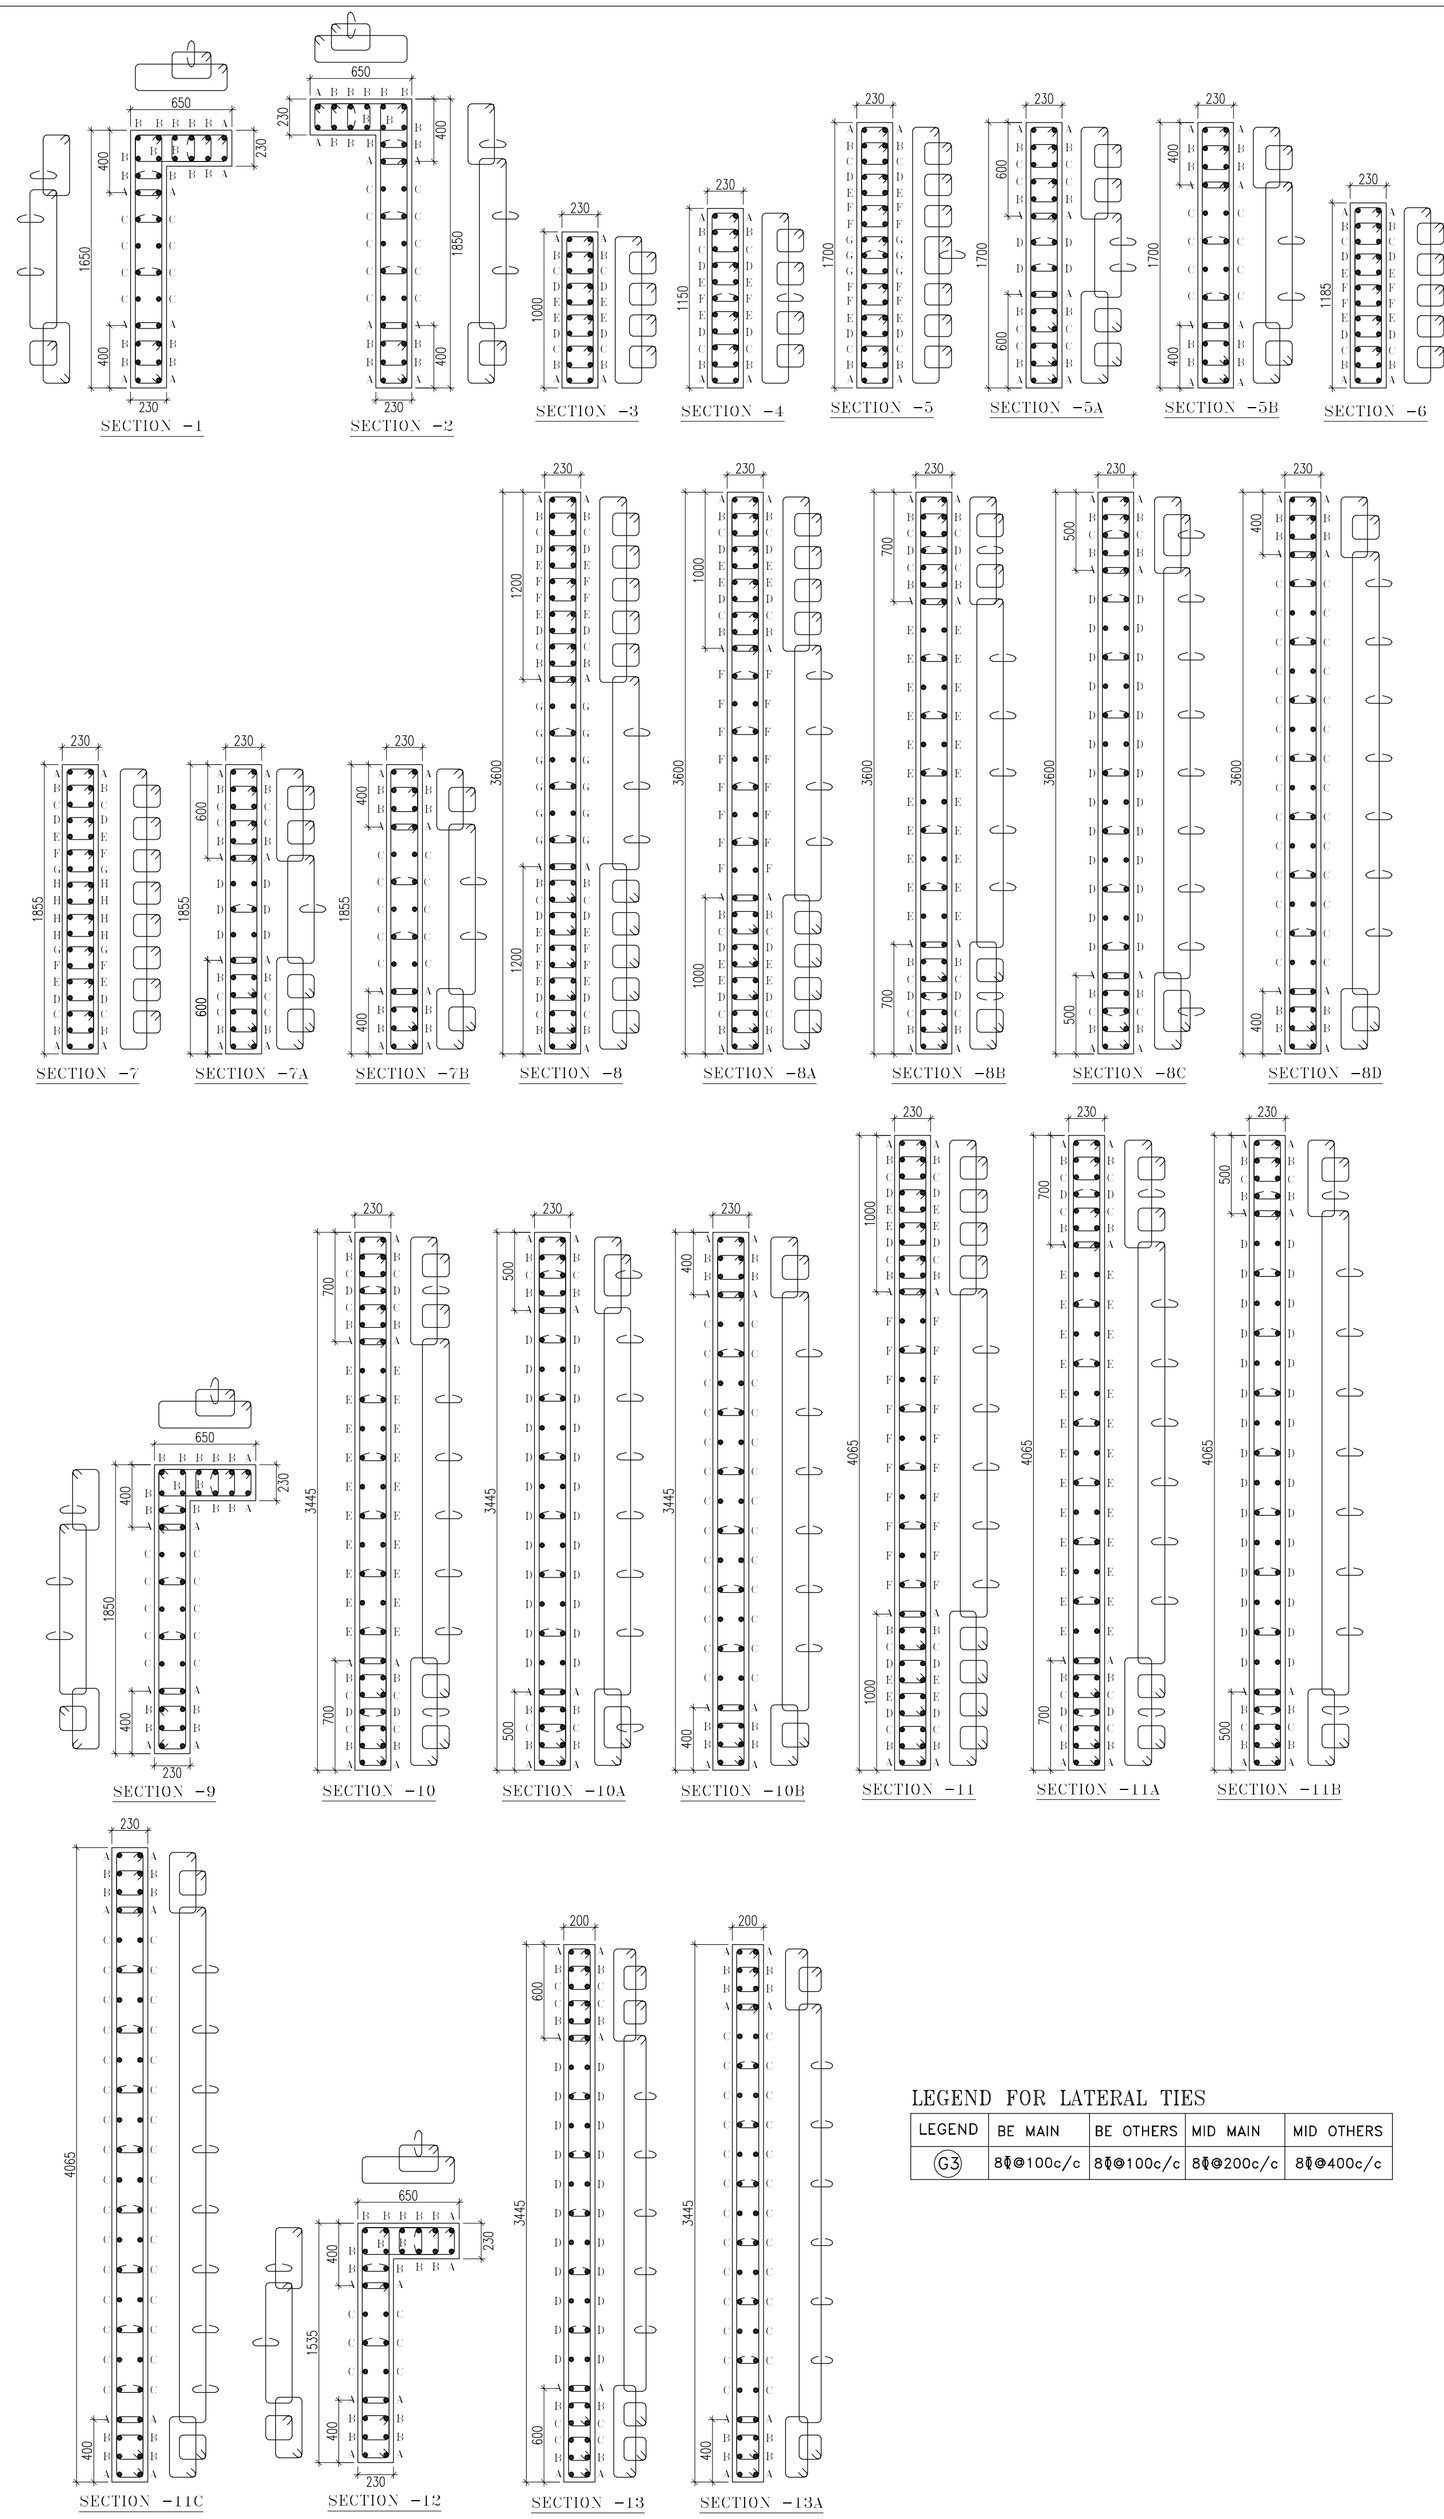

LEGEND FOR LATERAL TIES

LEGEND	BE MAIN	BE OTHERS	MID MAIN	MID OTHERS
G3	8⌀@100c/c	8⌀@100c/c	8⌀@200c/c	8⌀@400c/c

THIS DRAWING IS THE COPYRIGHT OF THE CONSULTANTS AND MAY BE USED OR REPRODUCED ONLY WITH HIS PRIOR PERMISSION.

##