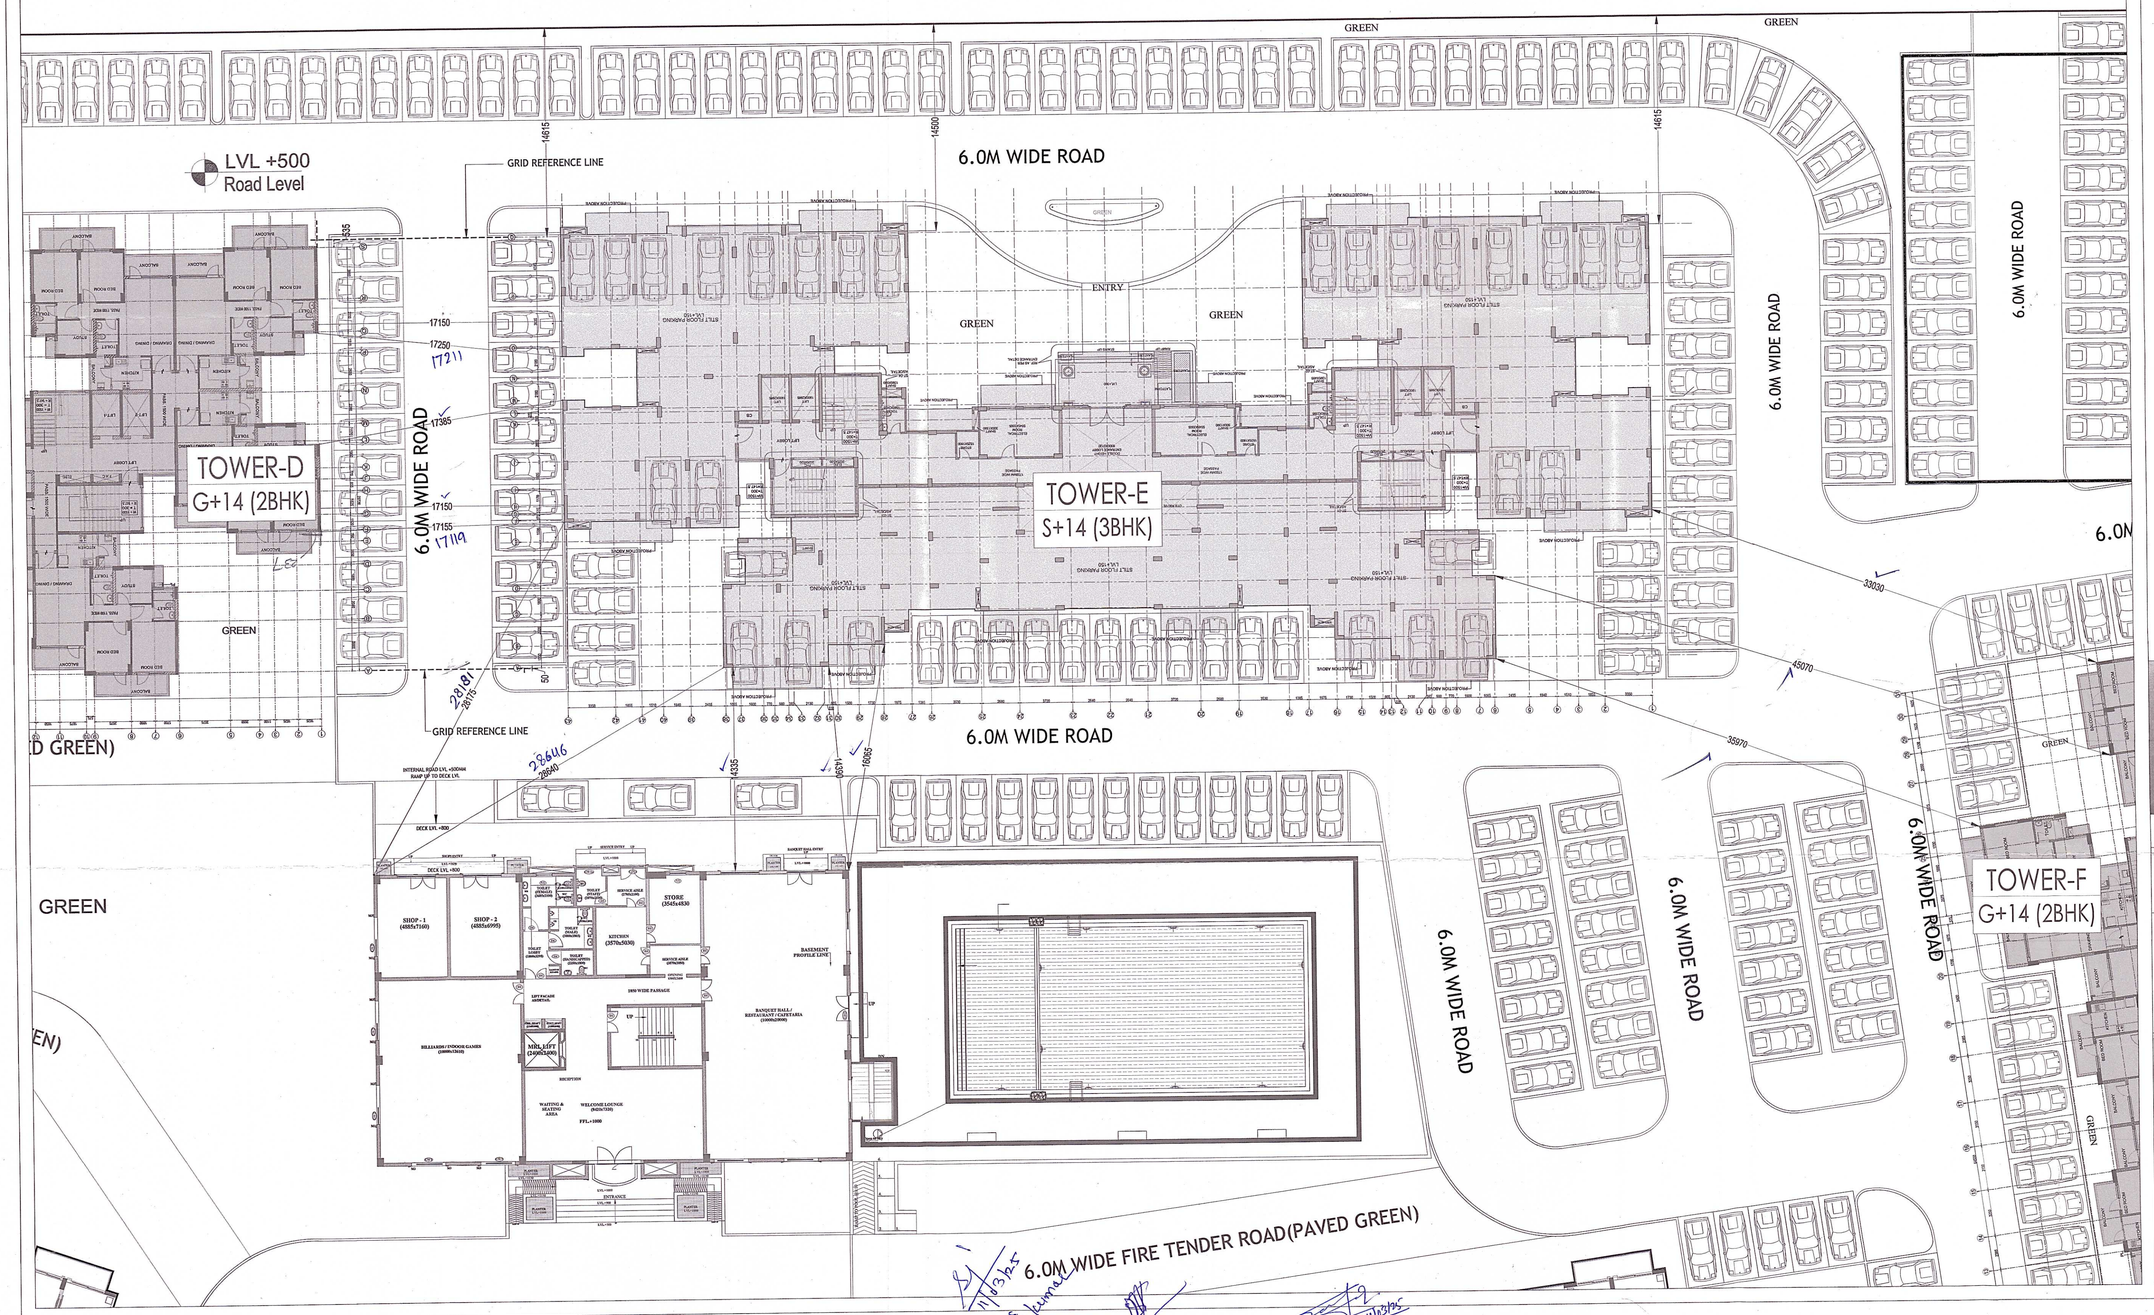


NOTES:
1. THIS DRAWING IS NOT TO BE SCALED. ONLY WRITTEN DIMENSIONS ARE TO BE FOLLOWED.
2. ALL DIMENSION SHALL BE CHECKED AT SITE BEFORE COMMENCEMENT OF WORK.
3. ANY DISCREPANCY MUST BE BROUGHT IN THE NOTICE OF ARCHITECT IMMEDIATELY.
4. THIS DWG. SHALL BE READ IN CONJUNCTION WITH STRUCTURE AND OTHER SERVICES DWG.

| S.NO. | DATE | REMARK |
|---|---|---|
| | | |
| | | |
| | | |
| | | |
| | | |

REVISIONS-:

OMAXE ARCH. PLANNING DEPT.
ADVANCE COPY | TENDER COPY | GOOD FOR CONSTRUCTION
DATE | SIGN

DATE- October 14, 2024

OMAXE
TURNING DREAMS INTO REALITY

PROJECT TITLE-:
TOWER E, AANANDA
PRAYAGRAJ

DRAWING TITLE-:
TOWER E
DEMARCATION LAYOUT

SCALE-NTS

DRAWING NO.
AANANDA/TOWER E/001

9997478384
11/03/25 (Karan Gradiya)

11/03/25 Gaurav Kumar (OMAXE)

Suresh Kumar Pandey. (OMAXE)

11/03/25 Sourav Saha (MARCO)