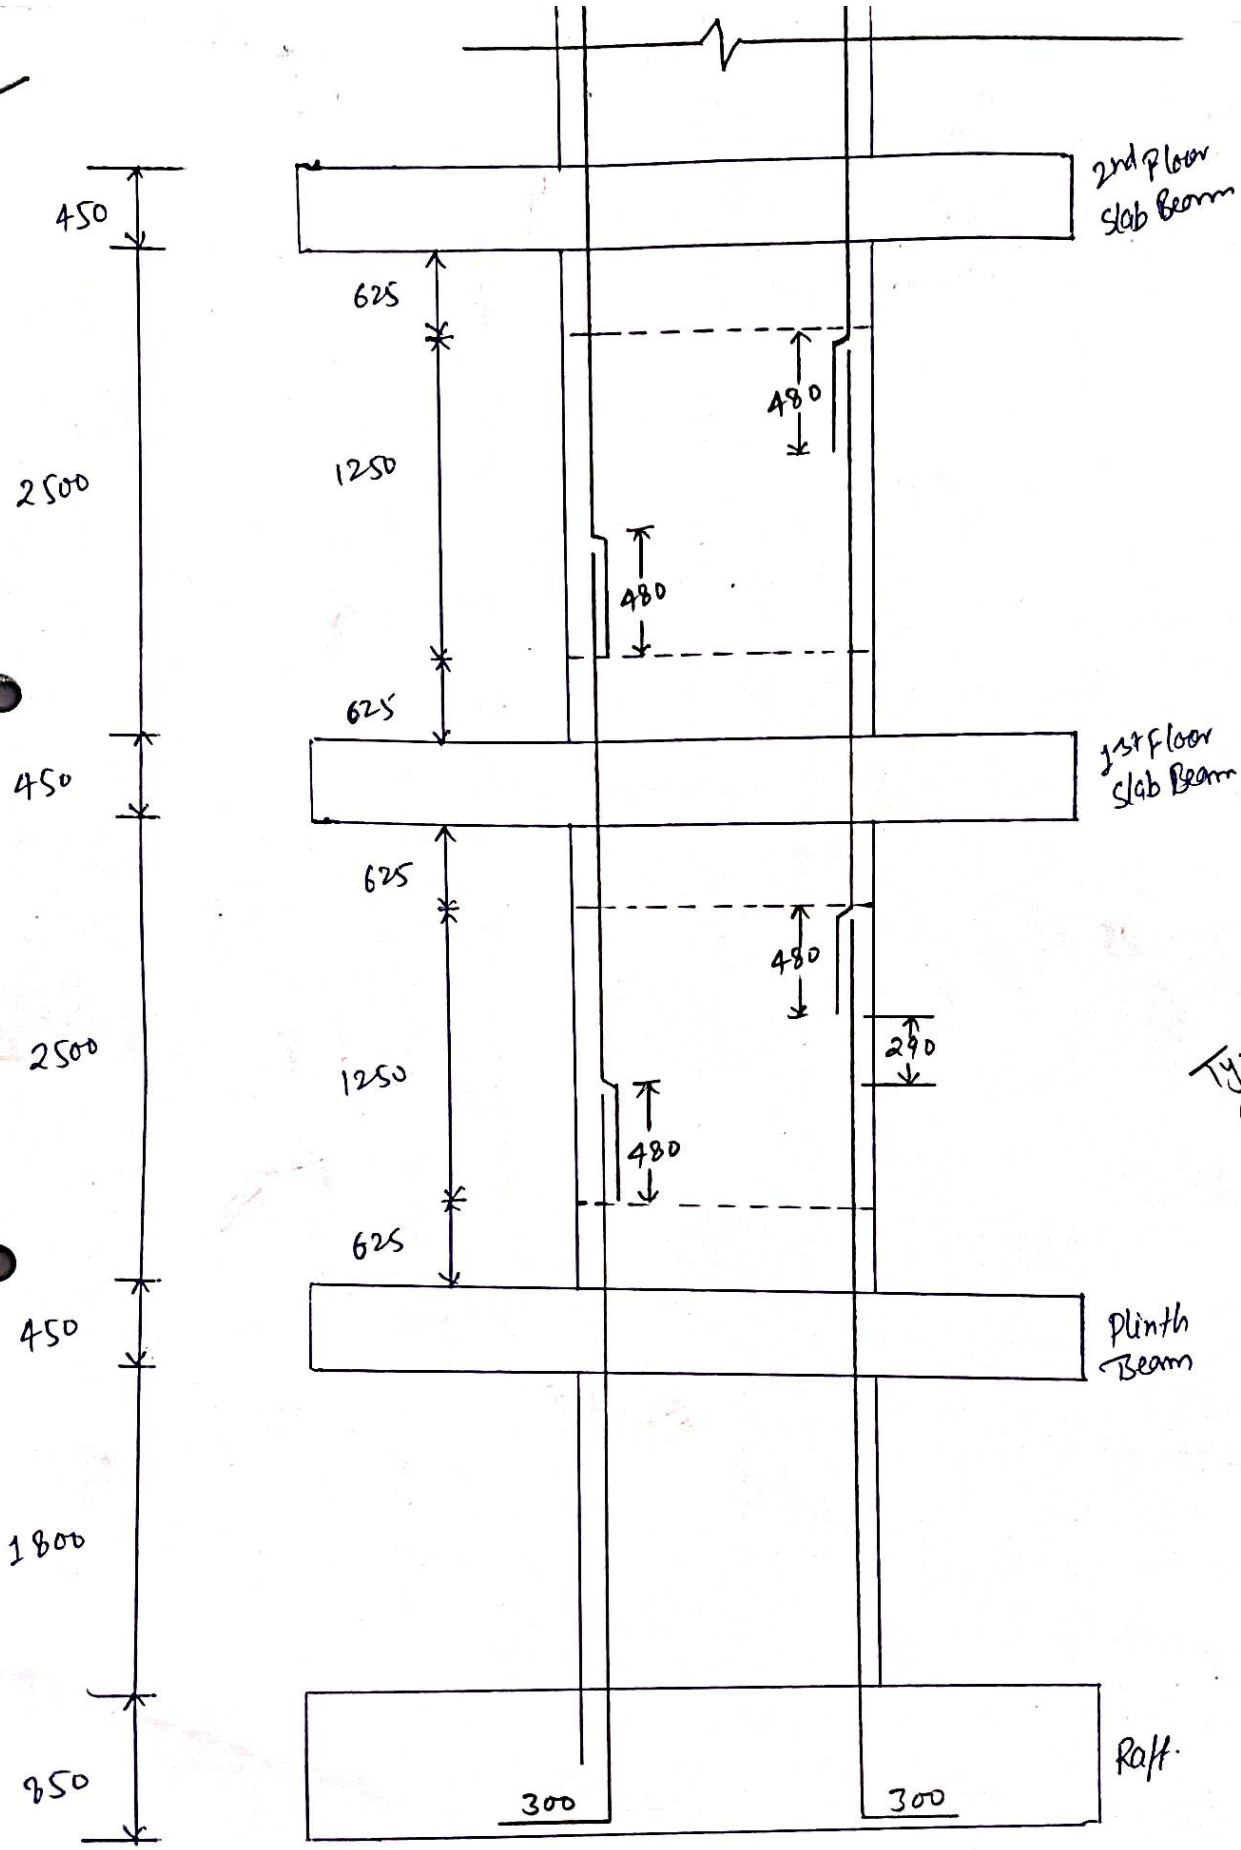


Typical = 3430 mm (12ϕ)

12ϕ (Raft to G.F Floor) = 4098 (743 + 1800 + 450 + 625 + 480)
12ϕ (Raft to G.F Floor) = 4868 (743 + 1800 + 450 + 625 + 1250)

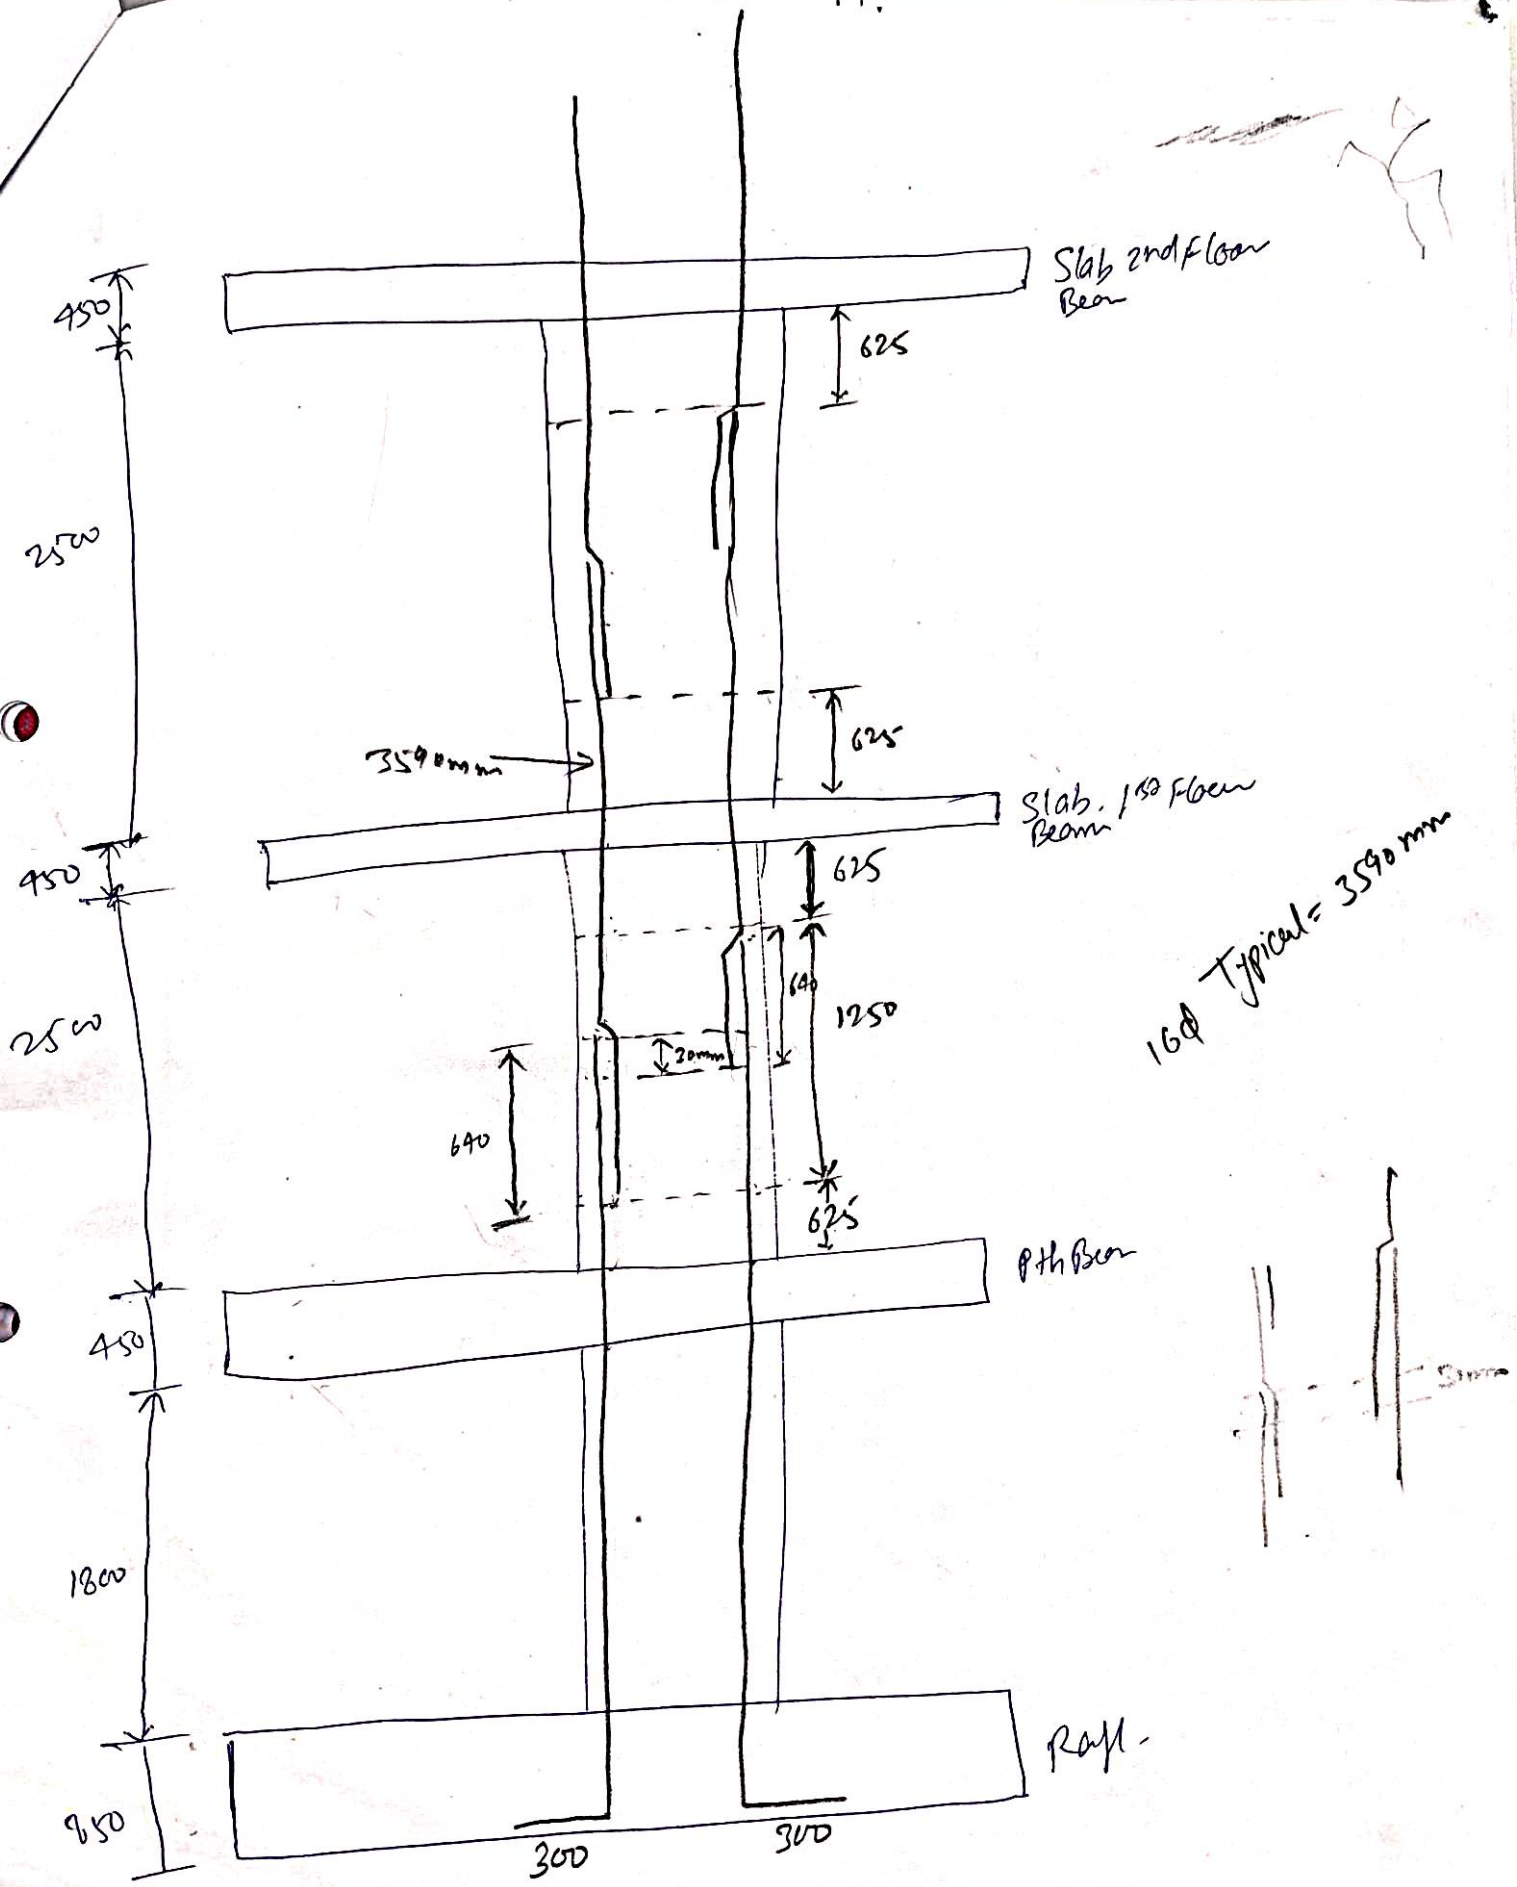


16ϕ = 4258 mm. (743+1800+450+625+640)
16ϕ = 4868 mm (743+1800+450+625+1250)

3 (18

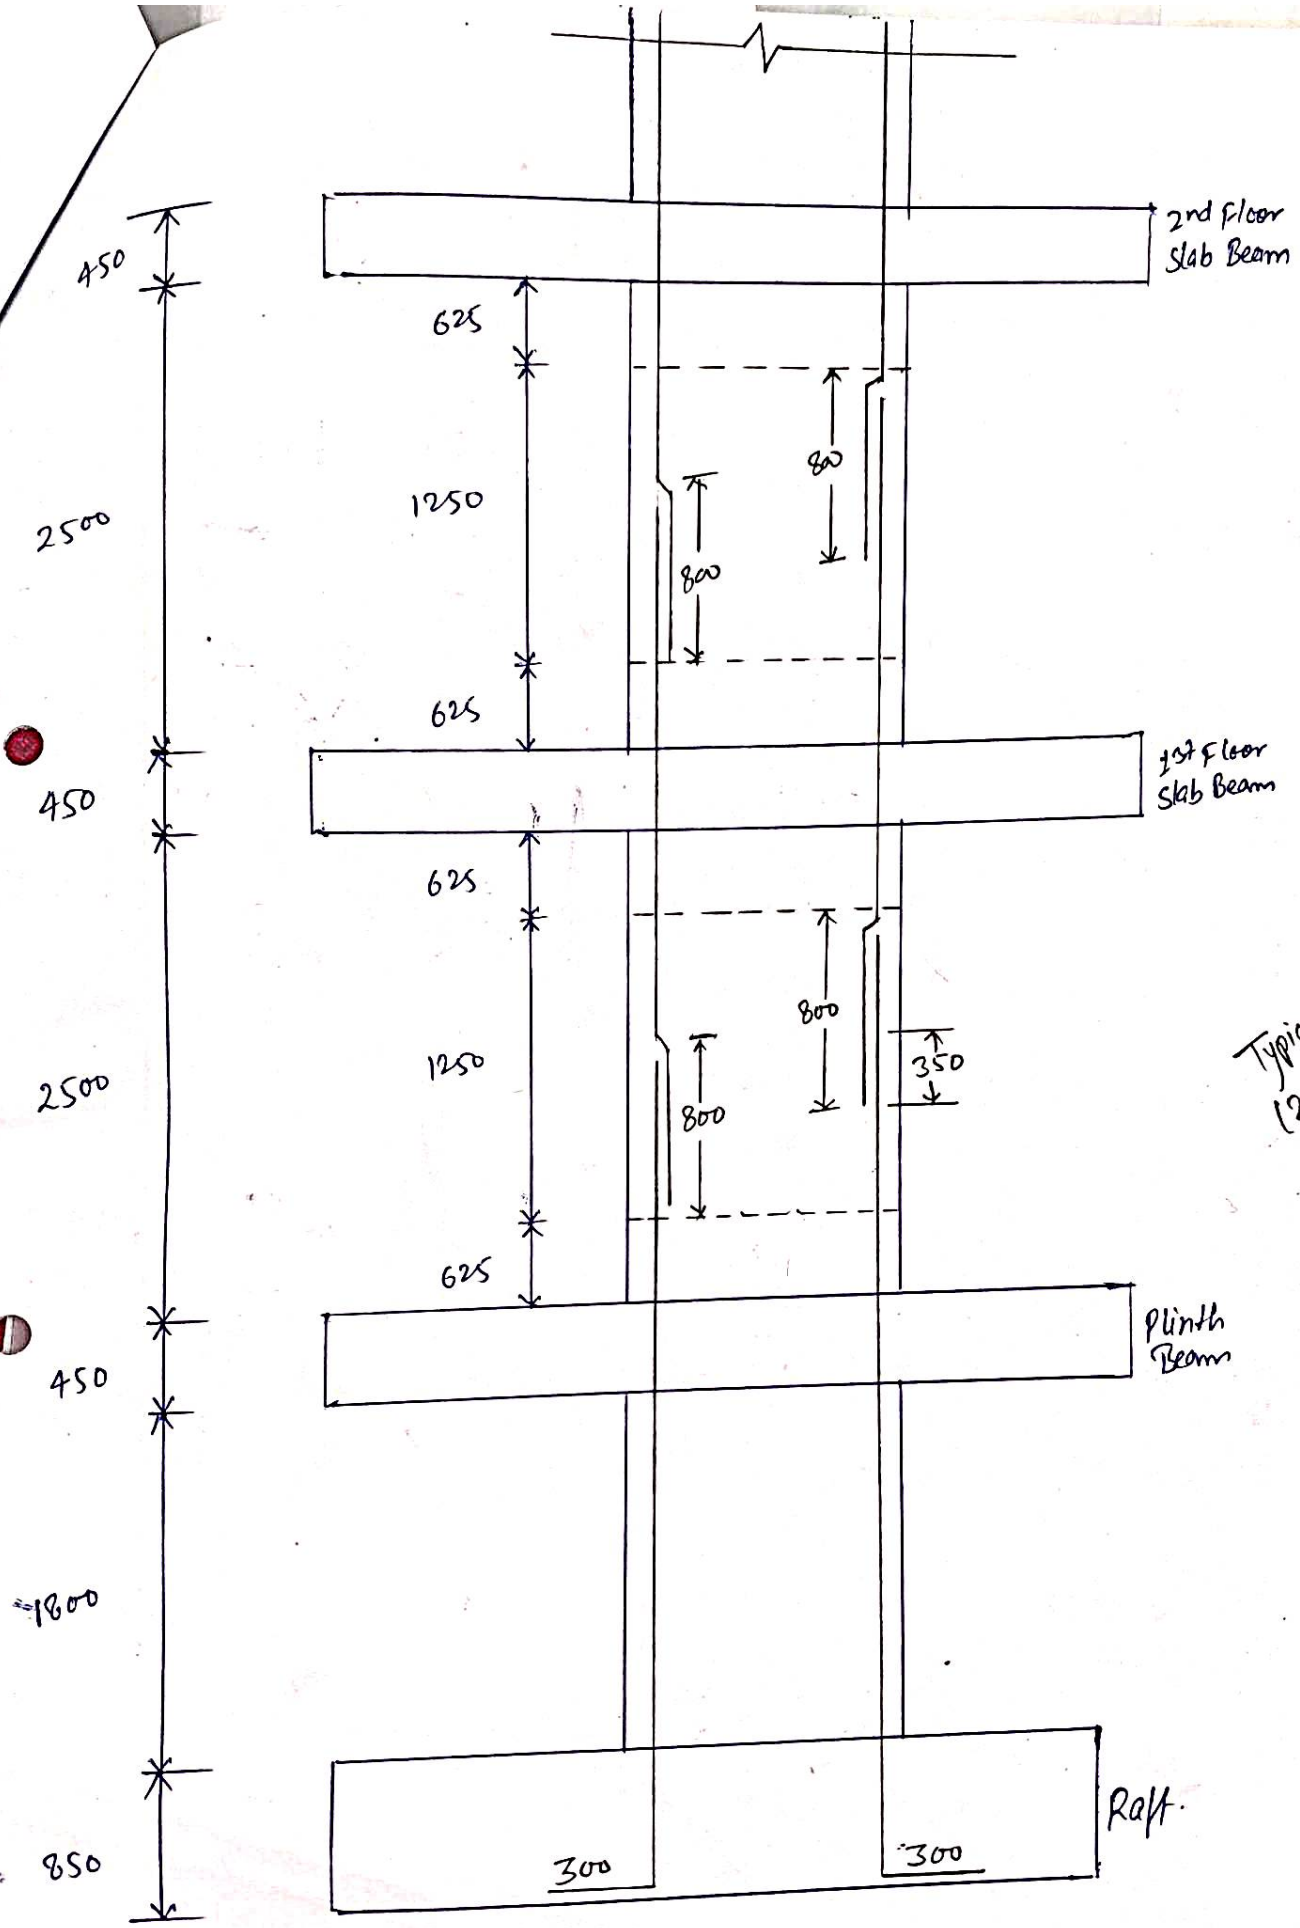


20ϕ (Raft to G.F Floor) = 4418mm (743 + 1800 + 450 + 625 + 800)

20ϕ (Raft to 1st Floor) = 4868mm (743 + 1800 + 450 + 625 + 1250)

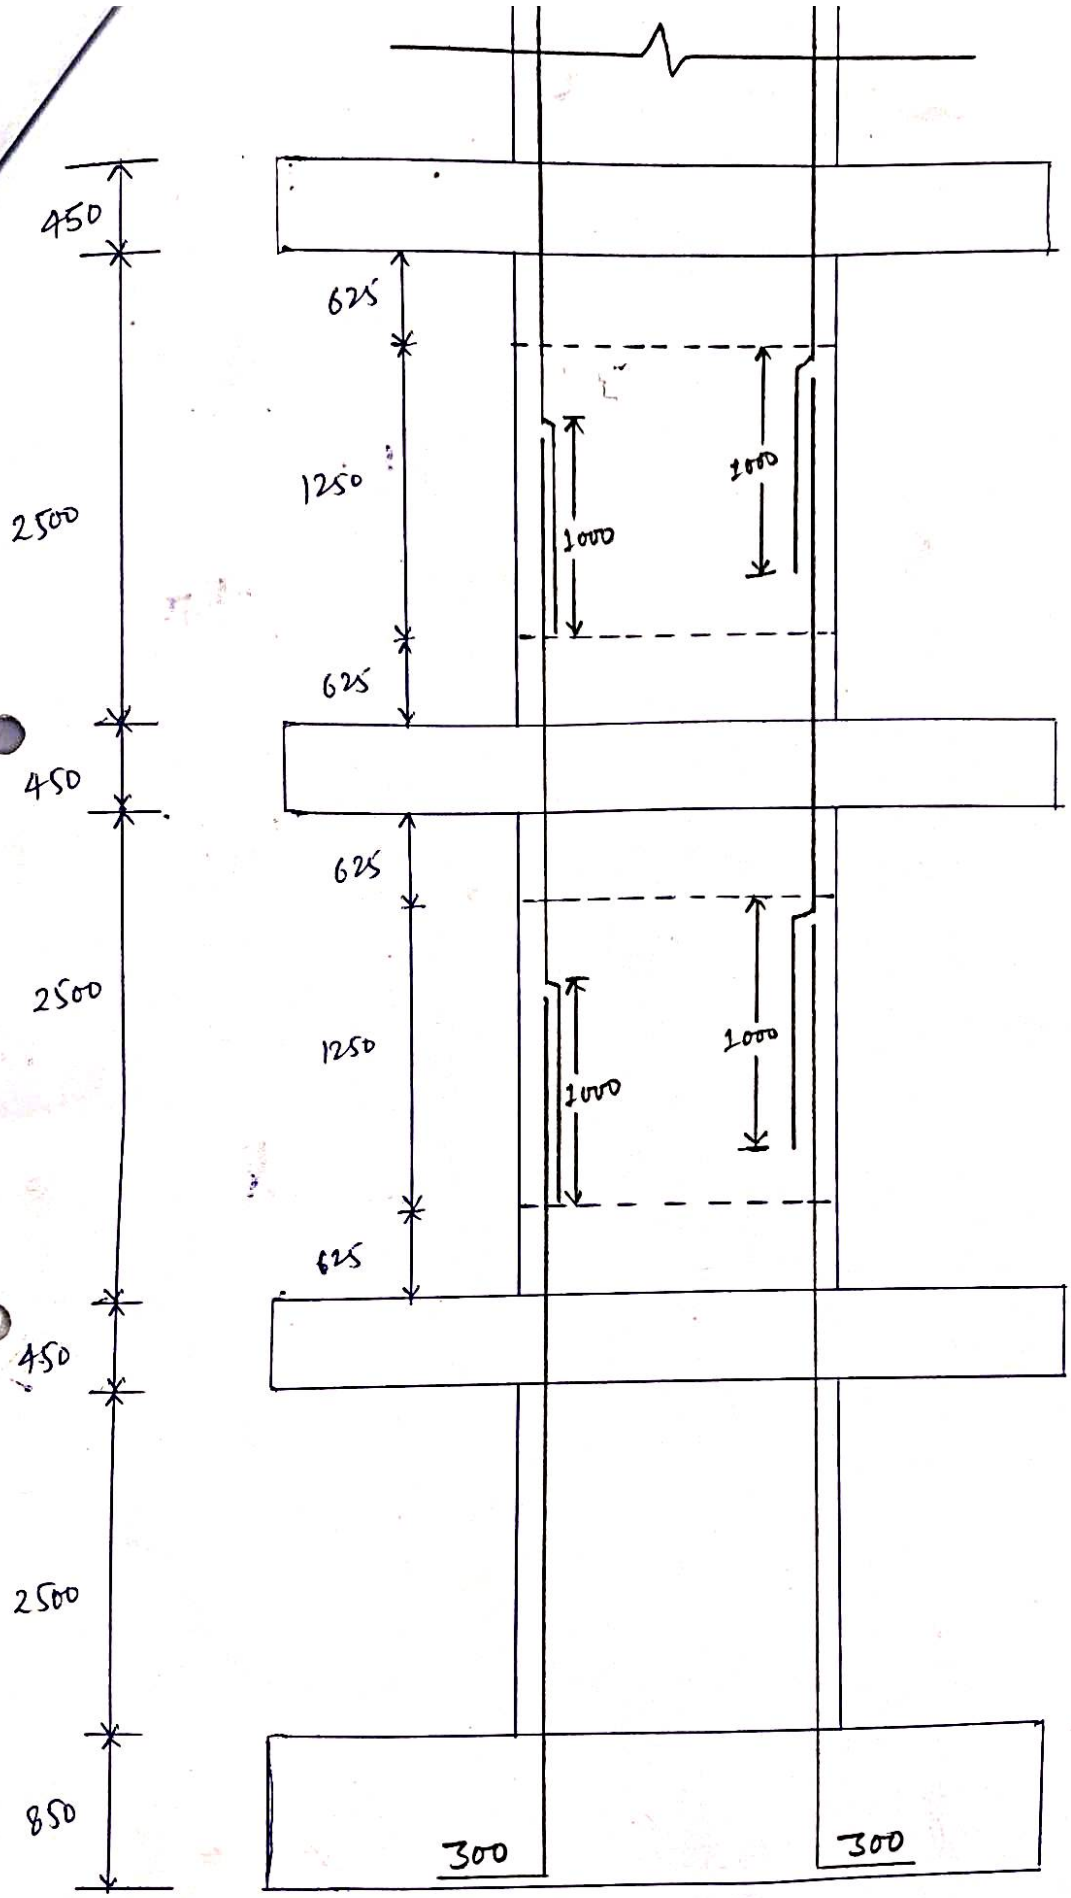


Typical = 3950 mm
(25Φ)

25Φ (Raft to G.F. floor) = 4618 (743+1800+450+625+1000)
25Φ (Raft to G.F floor) = 4868 (743+1800+450+625+1250)