01/06/25

Omaxe Aranda Tower - E Raft Outter Side Brick Work 115 mm Thk

Cont. - Marco Enterprises

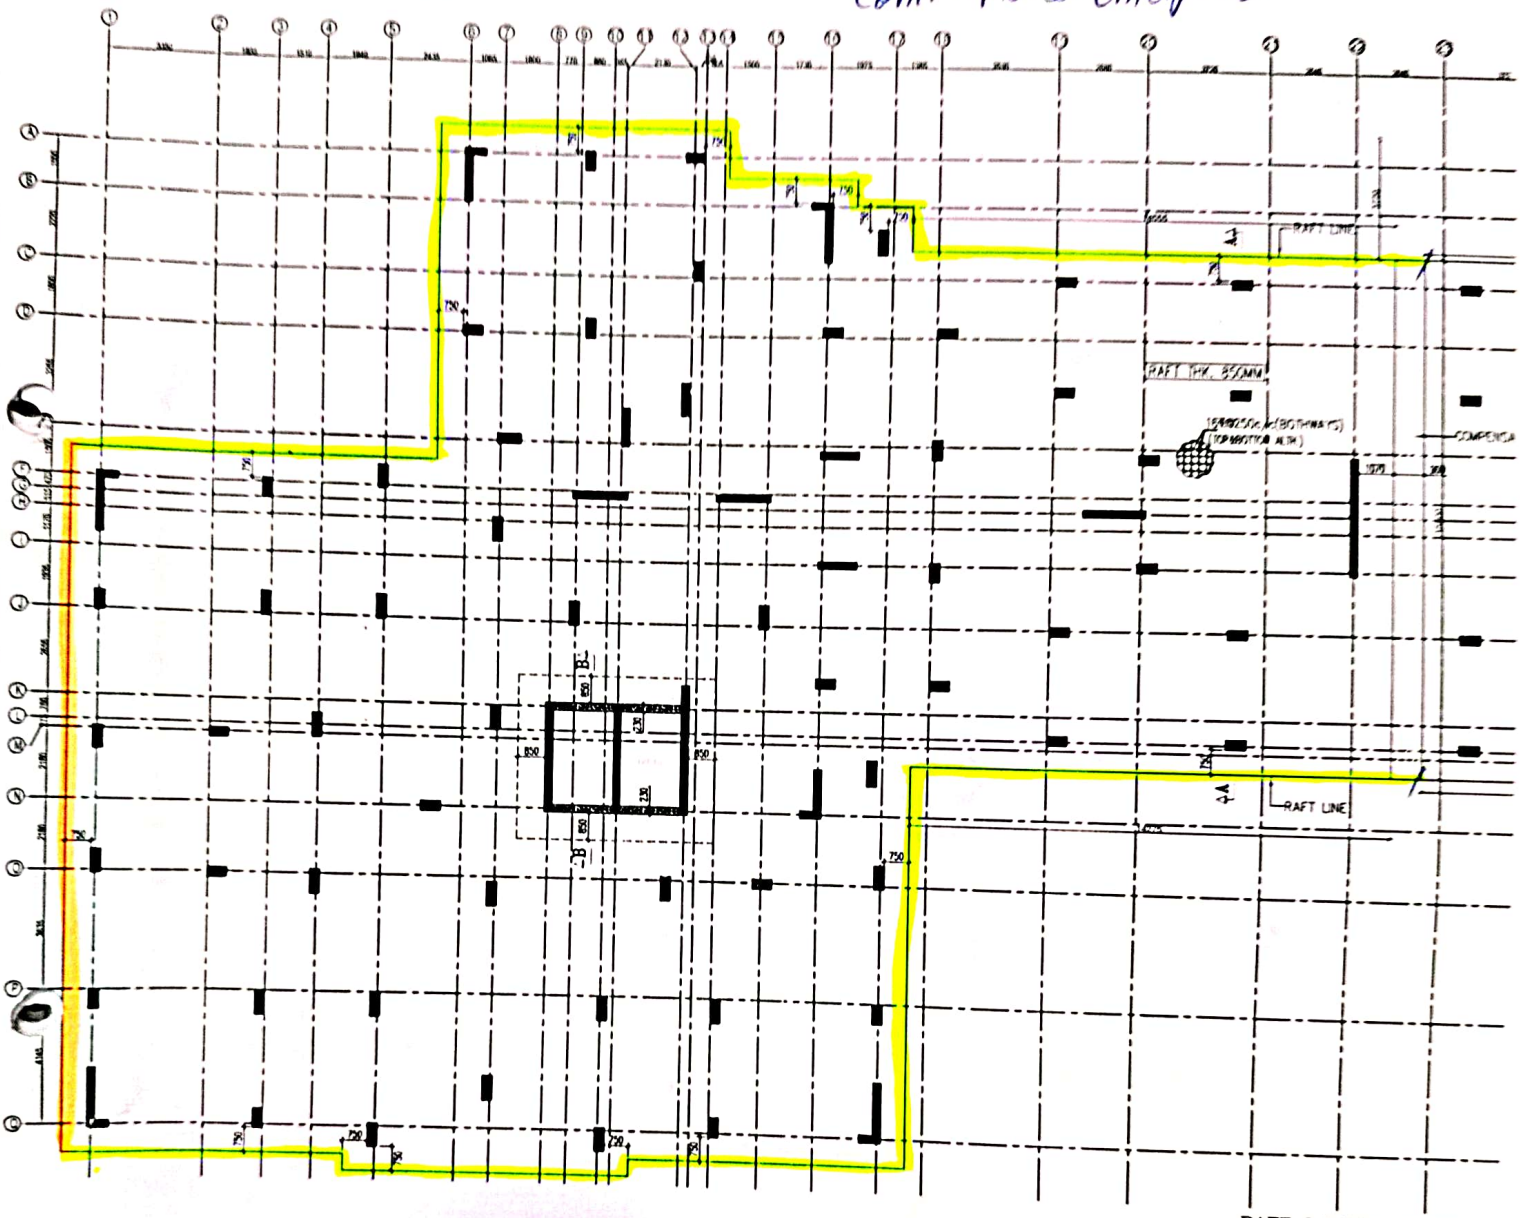

RAFT LAYOUT PLAN

300 mm Ht., 115 mm Thk Brick Work.

850 mm Ht., 115 mm Thk. Brick Work.

01/06/25

Marco - Enterprises

Omaxe Anamda
Tower-E Raft.
Grid (22'- 43)
Outter Side Brick
Work

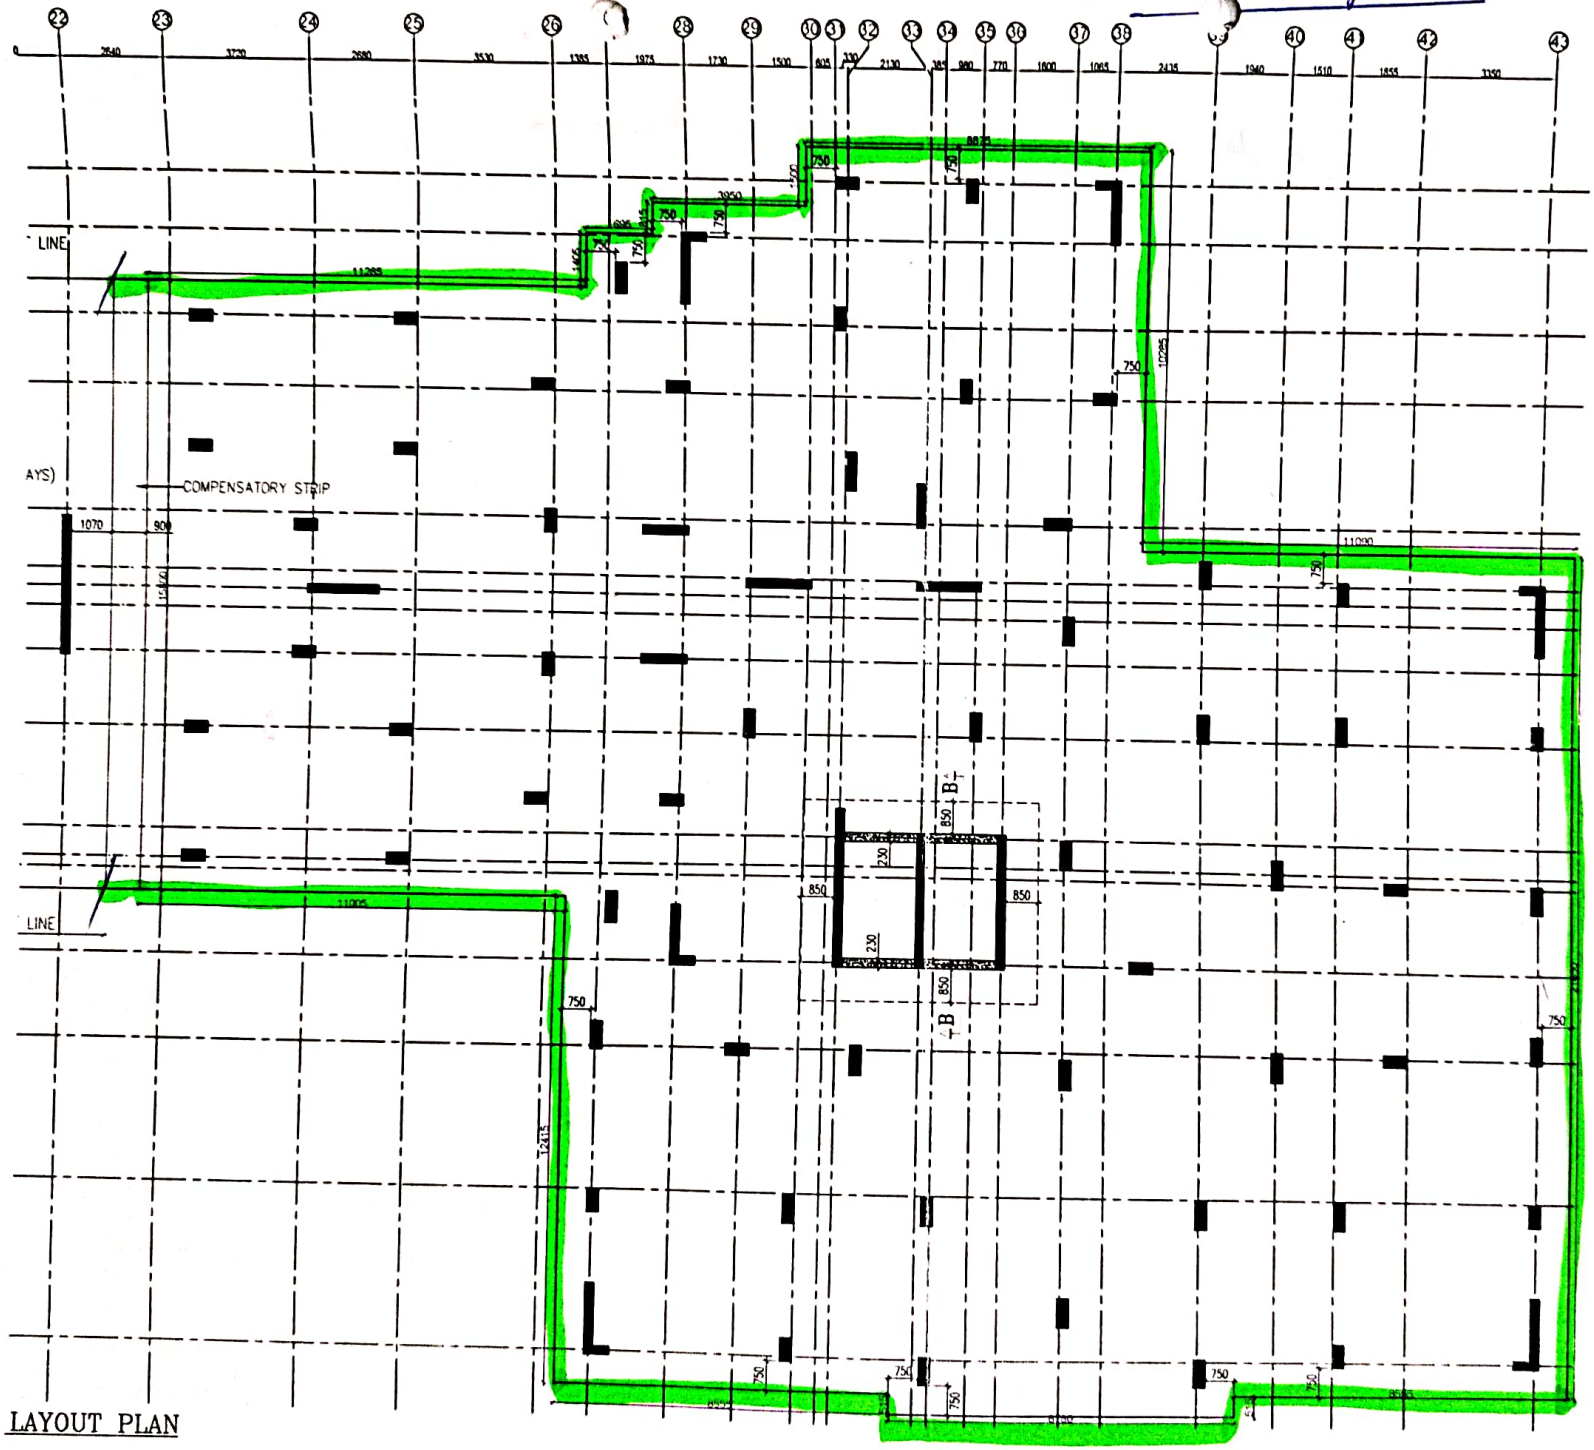

LAYOUT PLAN

300 mm Height
115 mm Thk
Red Brick Work

18/06/25

28/05/25

Omaxe Ananda
Tower-E
Prayagraj.
Raft PCC
measurement.

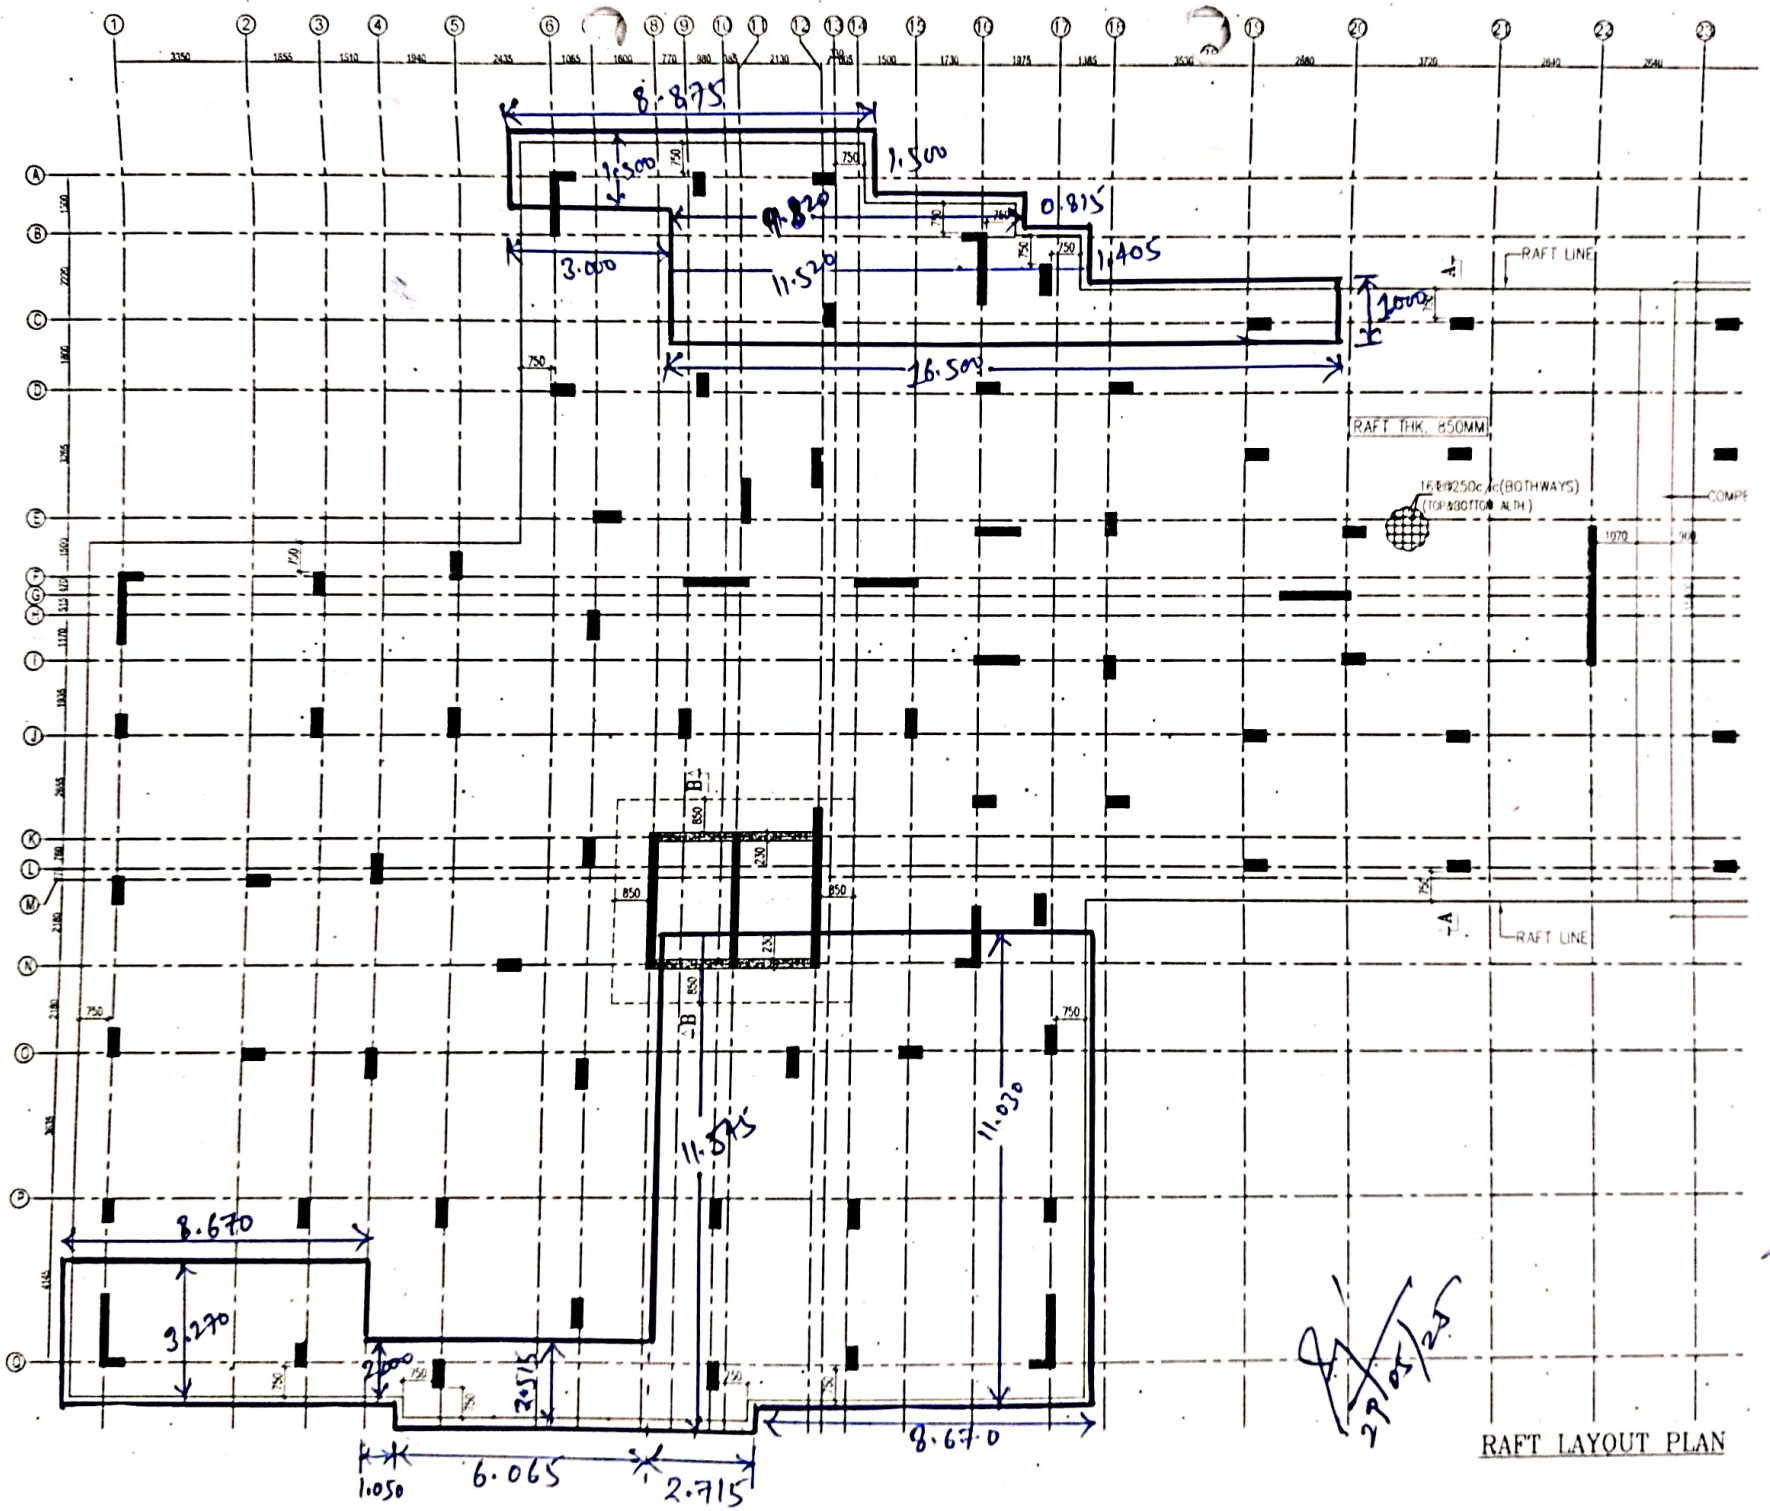

RAFT LAYOUT PLAN

PCC work
Done

29/05/25

29/05/25

13/05/25

Omaxe Tower-E
Prayagraj

Raft PCC Measurement

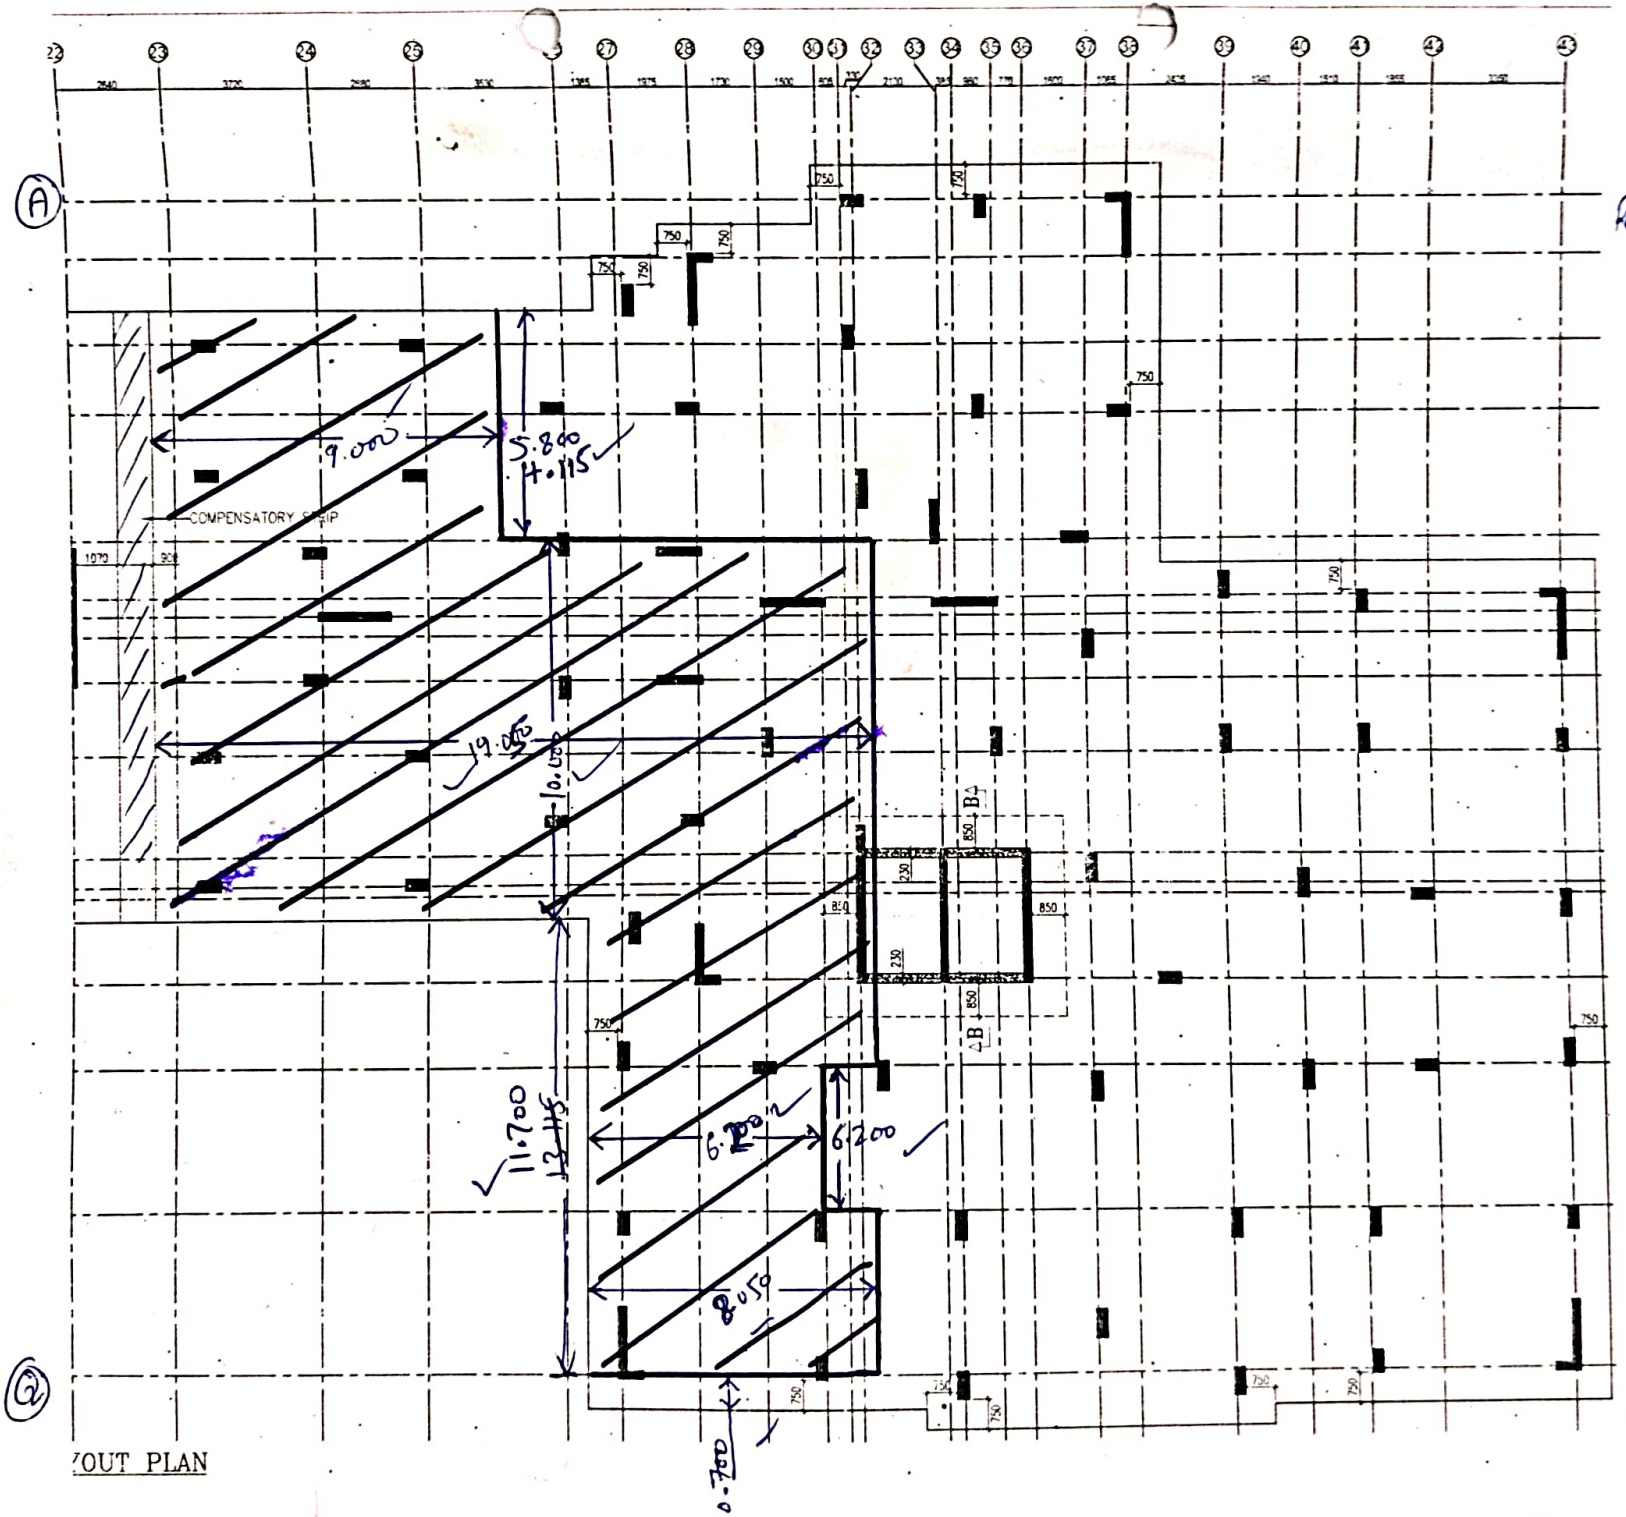

Existing Raft Line

Existing Raft Area

20/05/25

20/05/25

OUT PLAN

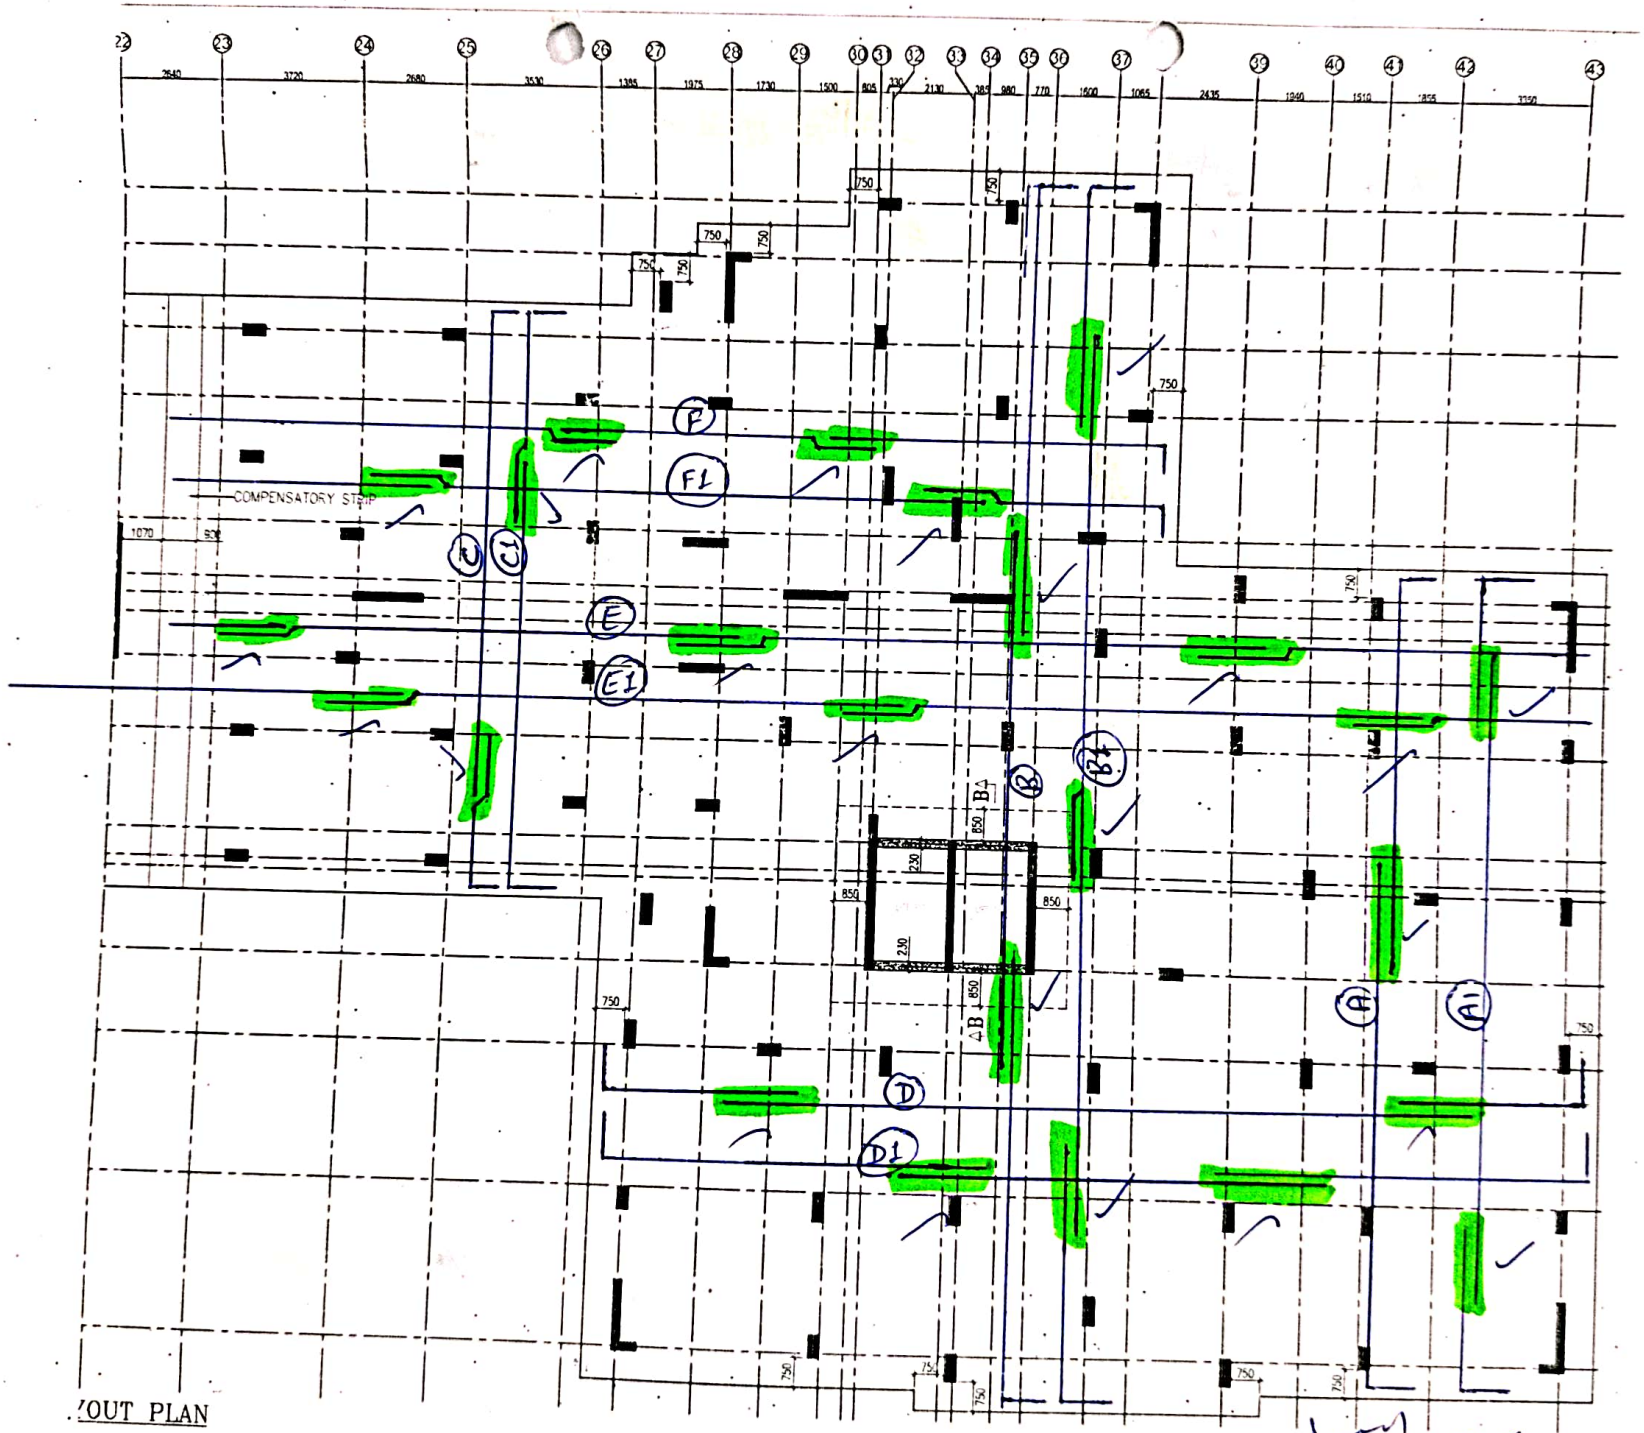

.OUT PLAN

Tower- E
Raft main & Dist. Bar lap schedule.

Raft Chair Size

950 ~~1150~~ mm

675 mm

675 mm

350 mm

350 mm

As per site

20/05/25

20/05/25

13/05/25

Ormare Tower-E, Prayagraj

Raft Excavation Measurement

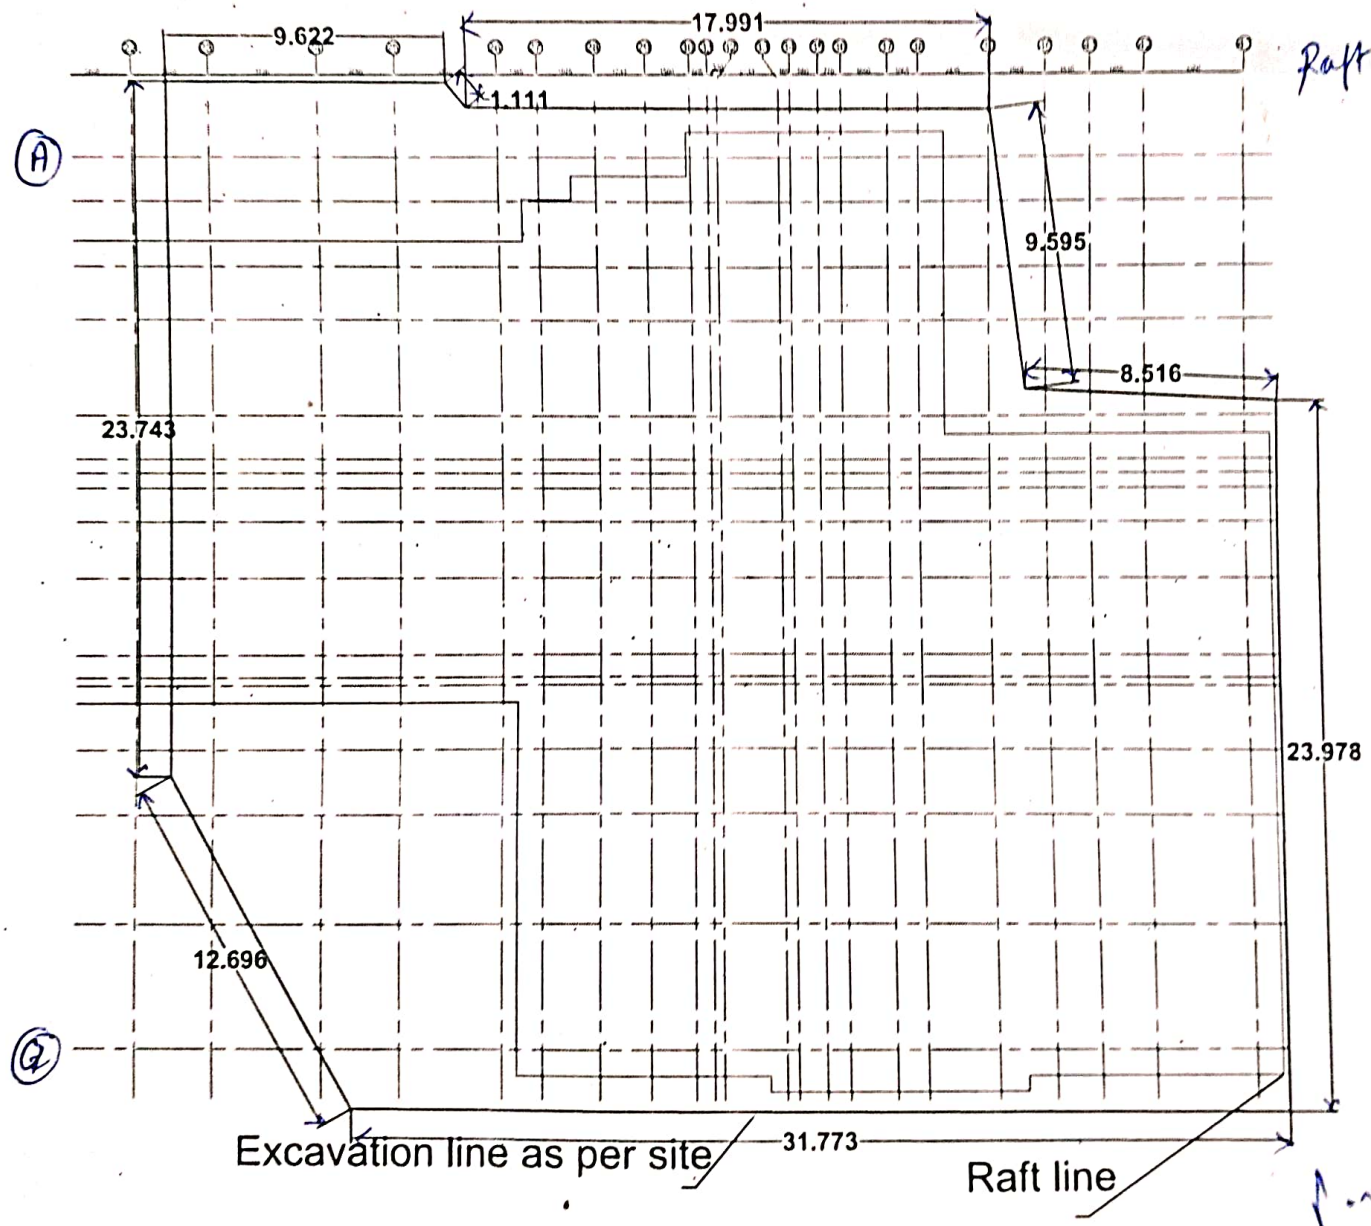

20-05/25

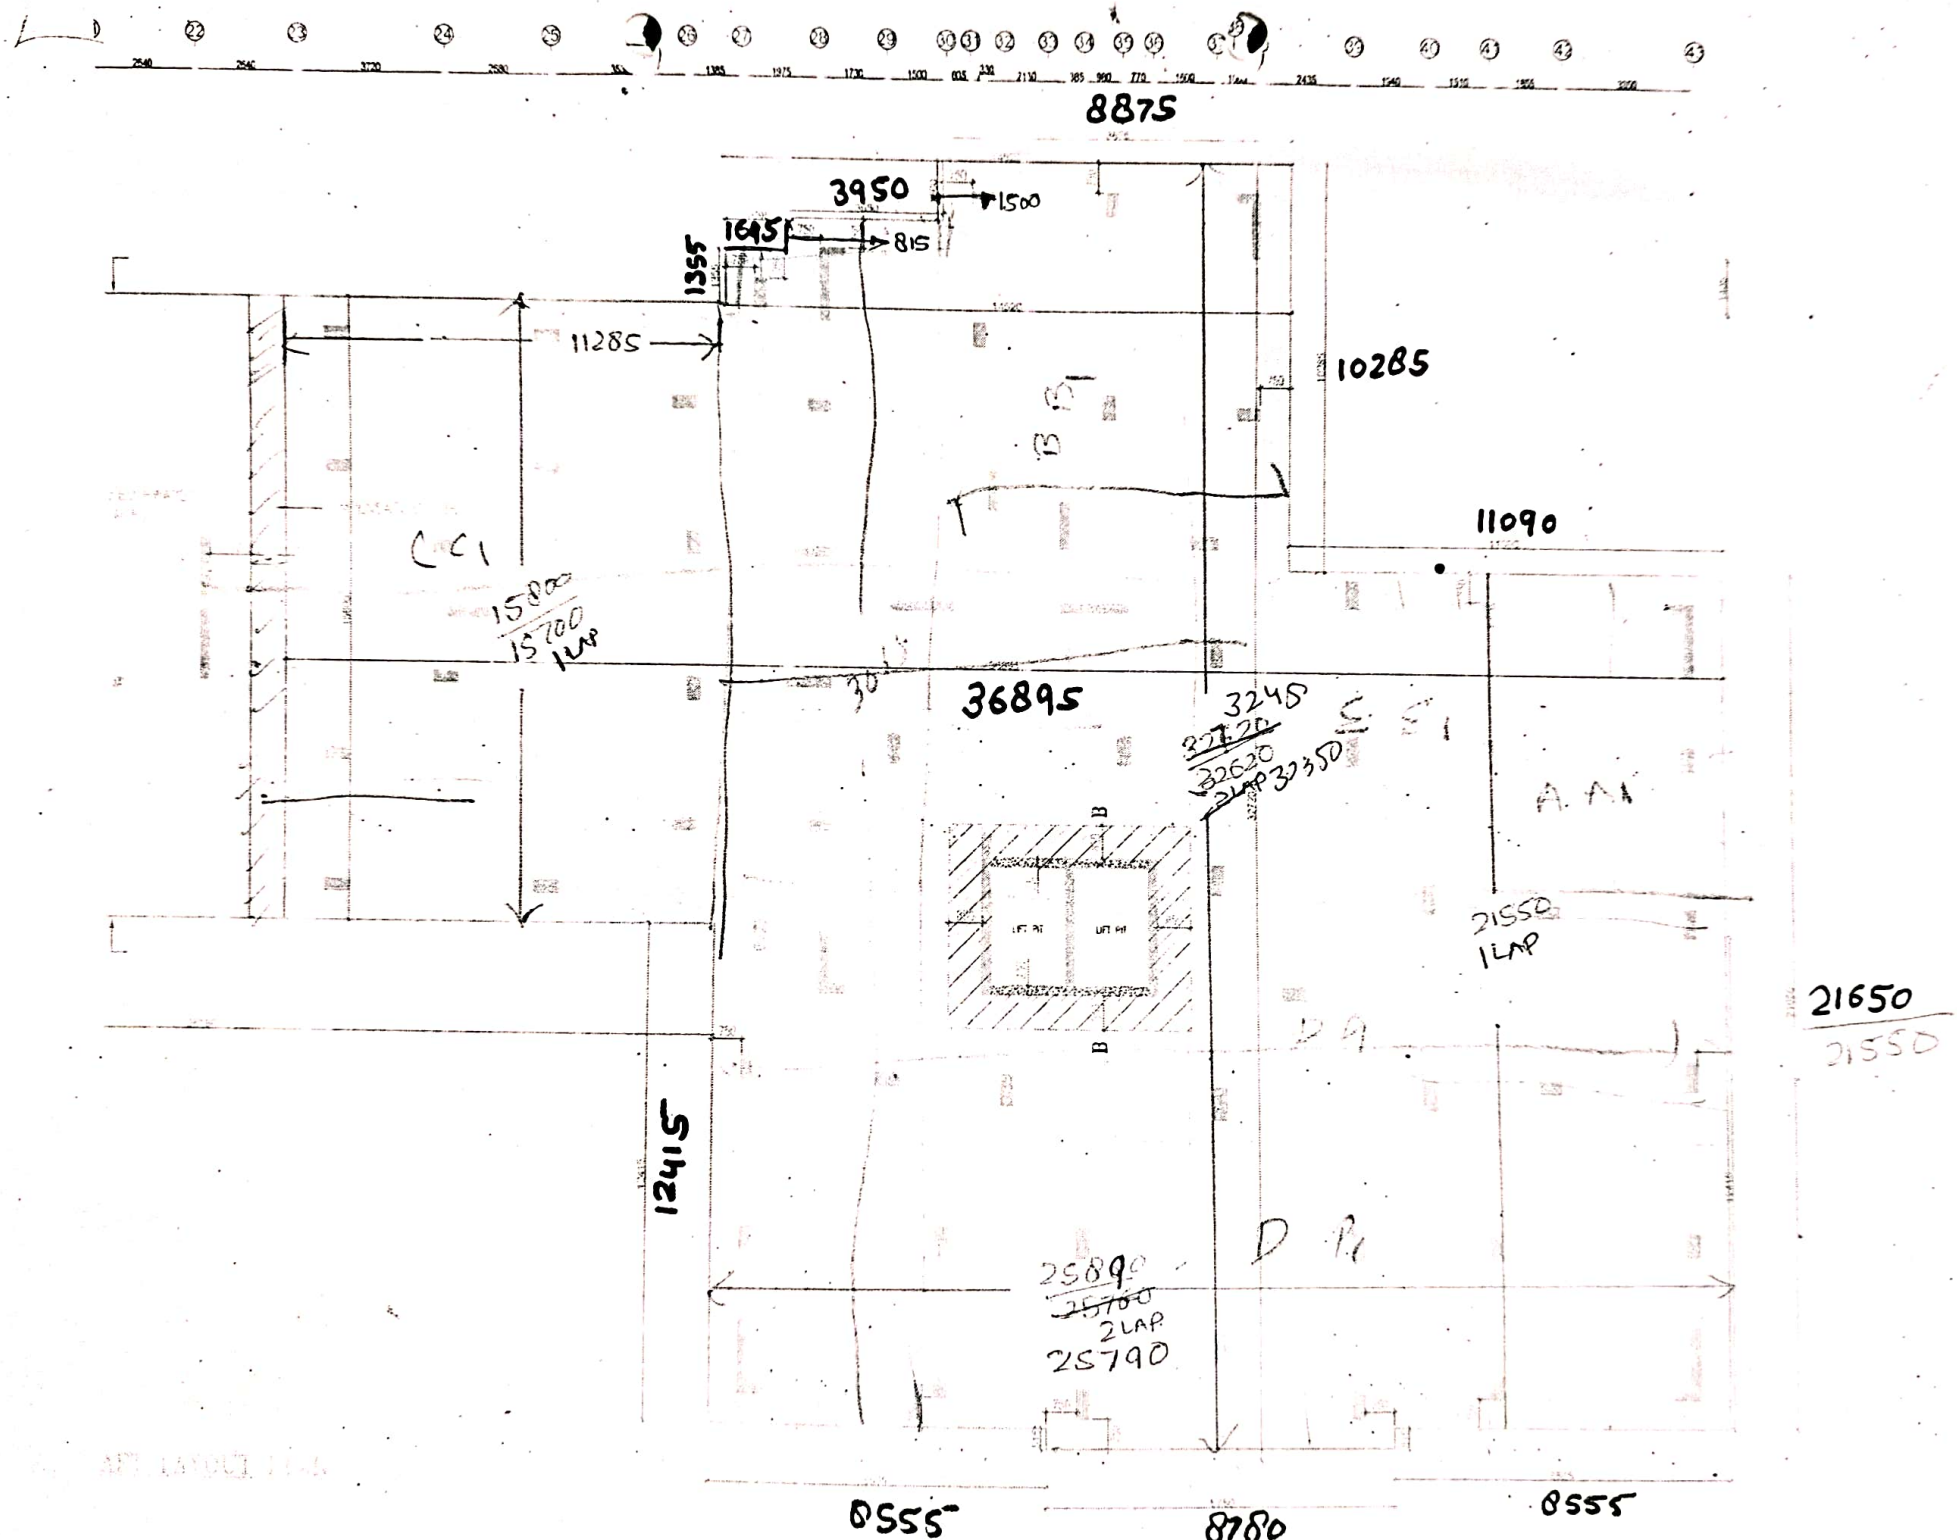
8875
3950
1500
1645
815
1355
11285
10285
11090
CC1
15800
15700
1LAP
36895
3248
32620
2LAP 32350
A.M
21550
1LAP
21650
21550
12415
25890
25700
2LAP
25790
8555
8780
8555

21550

A

A1

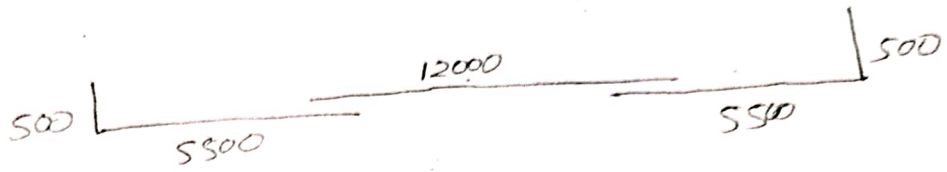

32620

B

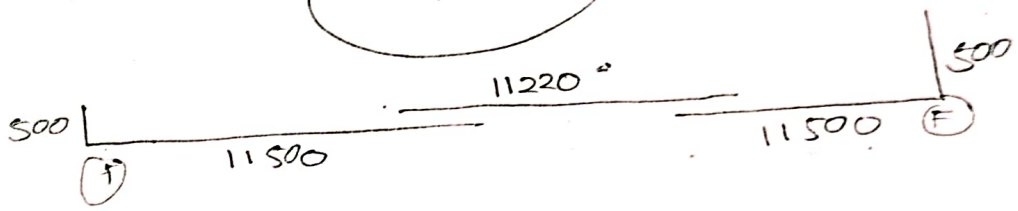

B1

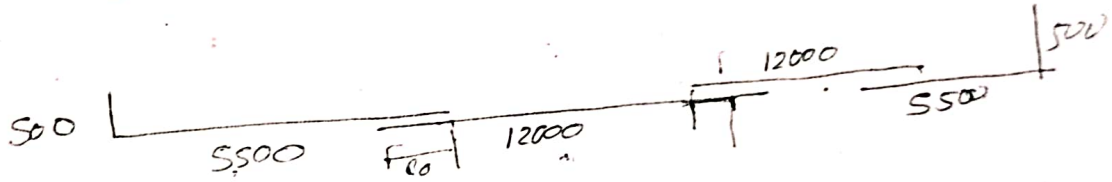

C C1

15700

C

C1

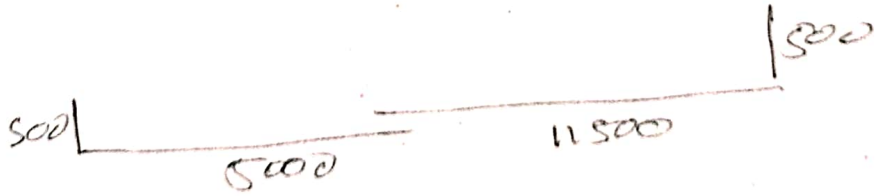

D D1 25790

D1

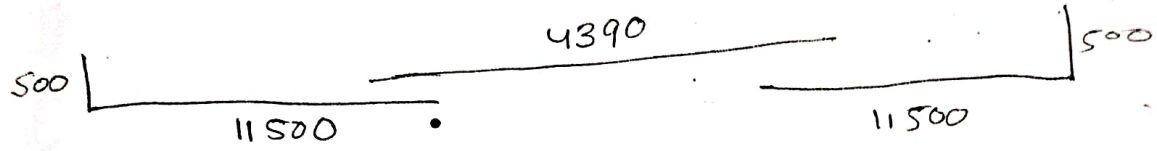

37645 E E1

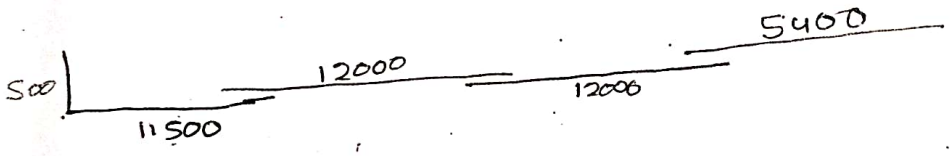

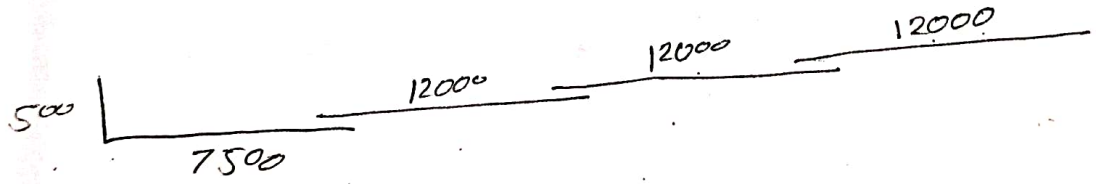

26655 25805+ 850

F F1

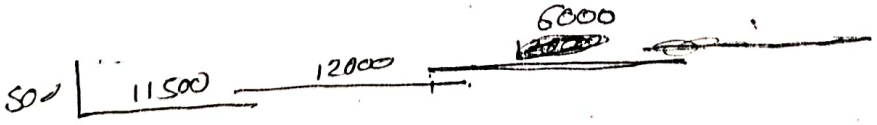

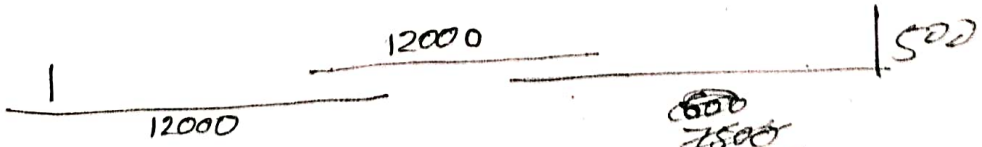

600
7500
8500

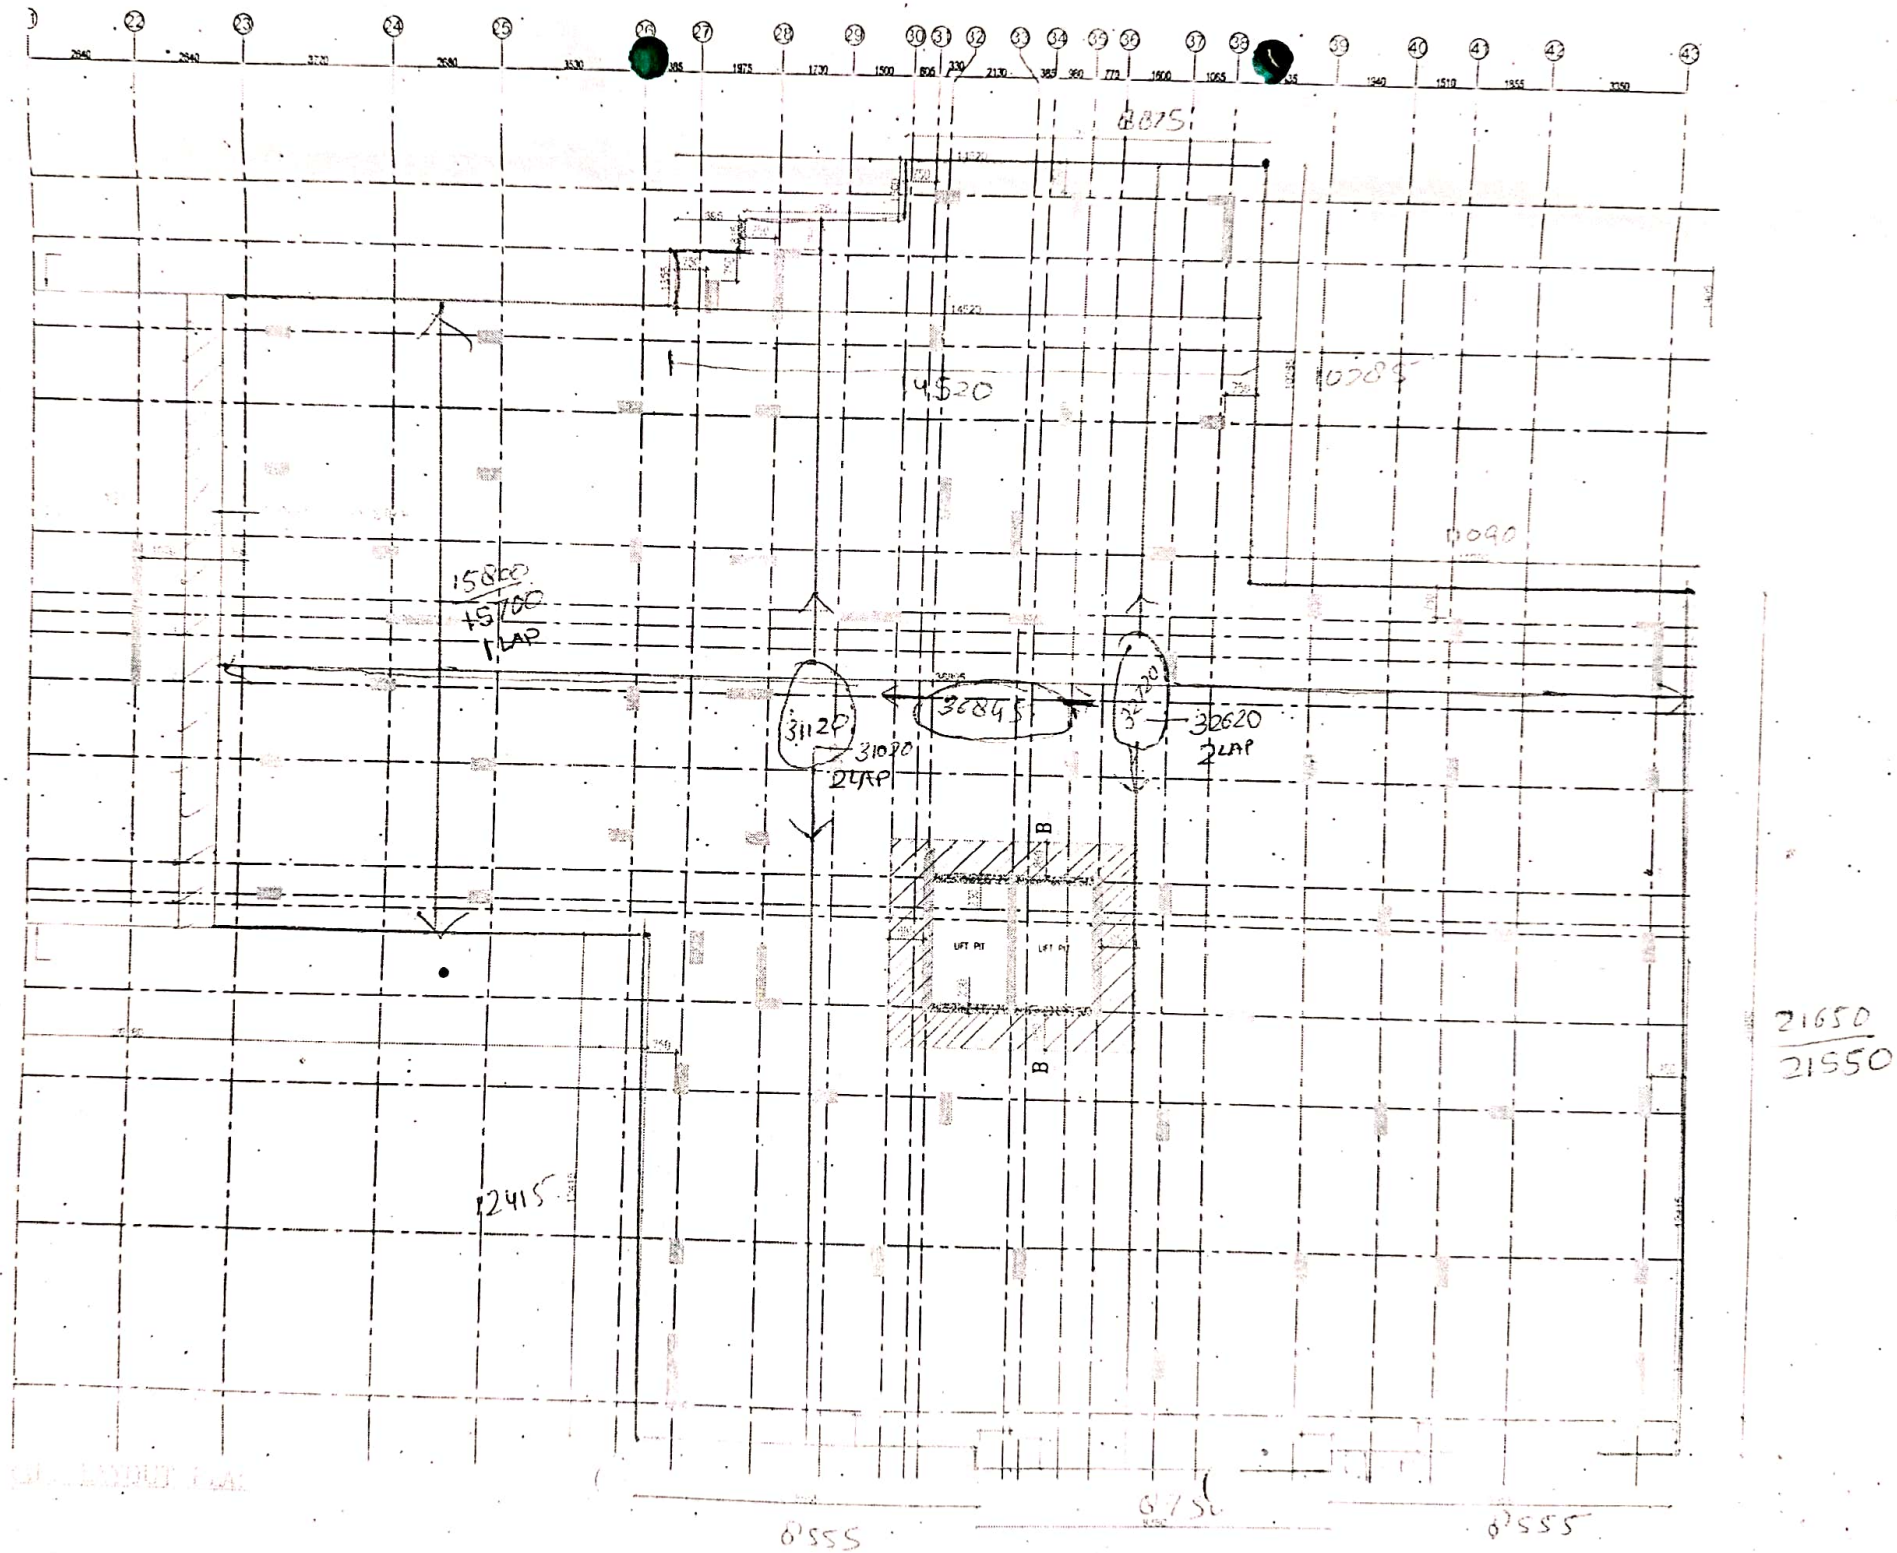
14520
15800
15700
1LAP
31120
31080
2LAP
30845
30620
2LAP
LIFT PIT
LIFT PIT
B
B
21650
21550
6555
6555